Rek. Tanah Kosong 26 Bebesen Simpang


DAFTAR ISIAN 206

Kantor / Rumah Dinas Peternakan

BADAN PERTANAHAN NASIONAL

8. Kantor / Rumah Dinas - Peternakan.

12

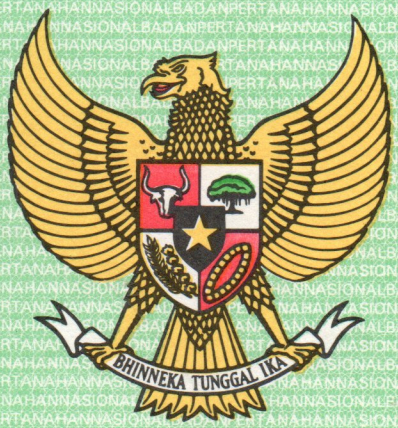



SERTIPIKAT

(TANDA BUKTI HAK)

Kec.	**: Kec. Bebesen**
No. Urut	**: 12**
Alamat	: Blang Kolak II
No. Sertifikat	: 01.09.02.09.4.00009
Tahun	: 15 Februari 2002
Peruntukan	: Tanah Syariat Islam/Rumah Dinas
SKPK	**: Dinas Syariat Islam**

KANTOR PERTANAHAN

KABUPATEN/KOTAMADYA

ACEH TENGAH

.....

AL 950340

01	09	02	09	4	00009

BADAN PERTANAHAN NASIONAL

"S E R T I P I K A T"

BUKU TANAH

HAK : PAKAI No. 9

PROPINSI : DAERAH ISTIMEWA ACEH

KABUPATEN/KOTAMADYA : ACEH TENGAH

KECAMATAN : BEBESEN

D E S A/KELURAHAN : BLENG KOLAK II

KANTOR PERTANAHAN
KABUPATEN/KOTAMADYA

ACEH TENGAH

DAFTAR ISIAN 208
No. 30 /12.2002

DAFTAR ISIAN 307
No. ..... /19....

AL. 950340

01 · 02 · 09 · 09 · A · 00009

PENDAFTARAN - PERTAMA

Halaman :

a) HAK PAKAI
No. 9
Desa BLANG KOLAK II

b) NAMA JALAN/PERSIL

c) ASAL PERSIL
1. Konversi
2. Pemberian hak Pakai
3. Pemisahan
4. Penggabungan

d) SURAT KEPUTUSAN
KEPALA KANTOR WILAYAH BPN
PROV. NANGGROE ACEH DARUSSALAM
NOMOR. 4/HP/BPN/ 2002.
Tgl. 28 Januari 2002

Uang pemasukan/biaya administrasi

Lamanya hak berlaku
Selama masih dipergunakan.
Berakhirnya hak
Tgl.

e) SURAT UKUR / GAMBAR SITUASI
Tgl. 18 Agustus 2001
No. 09
Luas 12.251 M2.

f) NAMA PEMEGANG HAK
PEMERINTAH KABUPATEN ACEH TENGAH BERKEDUDUKAN DI-TAKENGON.-

g) PEMBUKUAN
Takengon Tgl. 15 Pebruari 2002
Kepala Kantor Pertanahan
Kabupaten/Kotamadya
ACEH TENGAH
ttd
=. DRS. BUDI YAZIR .=
NIP 010172837

h) PENERBITAN SERTIPIKAT
Takengon Tgl. 15 Pebruari 2002
Kepala Kantor Pertanahan
Kabupaten/Kotamadya
ACEH TENGAH
=. DRS. BUDI YAZIR .=
NIP 010172837

i) PENUNJUK

DAFTAR ISIAN 207

01	09	02	09	4	00009

Nomor hak : 9

SURAT UKUR

~~GAMBAR SITUASI~~

NIB.01.09.02.09.00023

Nomor : 09 /19 2000.-

SEBIDANG TANAH TERLETAK DALAM

Propinsi : Daerah Istimewa Aceh

Kabupaten/~~Kotamadya~~ : Aceh Tengah

Kecamatan : Bebesen

Desa/~~Kelurahan~~ : Blang Kolak II

Peta : Garis

Lembar : 34.45 Kotak : A.B.5 A.B. 1 Nomor Pendaftaran : .....


Keadaan Tanah : Sebidang tanah yang diatasnya terdapat Bangunan Kantor /Rumah Dinas Perternakan Kabupaten Aceh Tengah

Tanda-tanda batas : Pagar kawat berduri.

Luas : 12.251 M2. (Dua belas ribu dua ratus lima puluh satu meter persegi)

Penunjukan dan penetapan batas : .....

PERBANDINGAN 1 : 1000

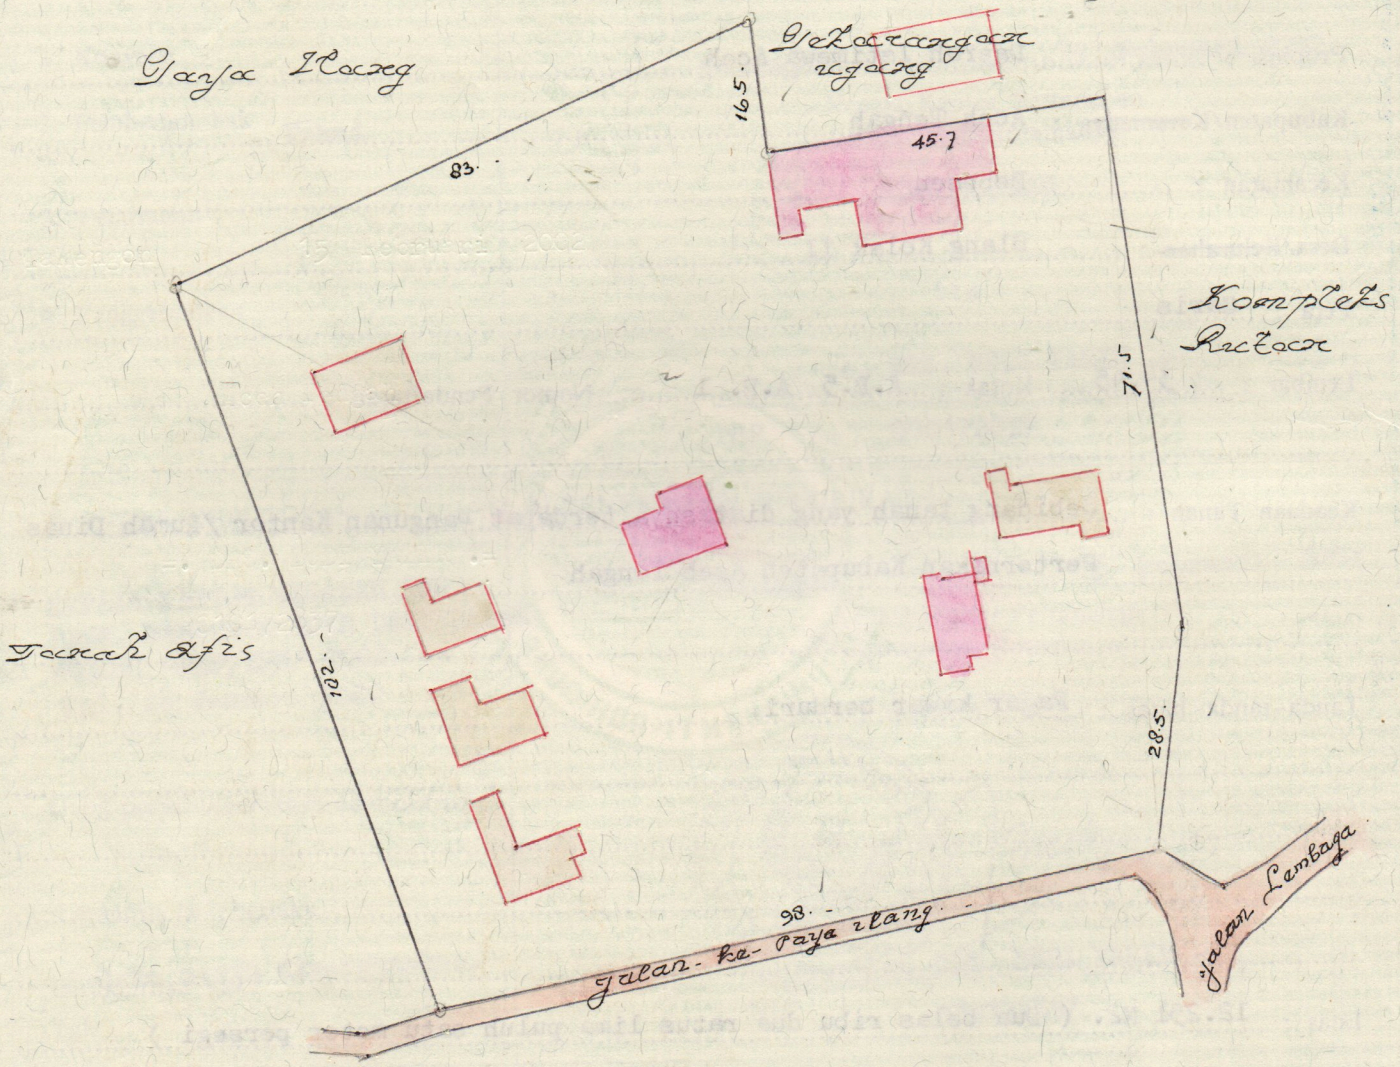

PENJELASAN : ..... batas tanah ini

Hal lain-lain : .....

.....

.....

.....

Daftar Isian 302 tgl. 8 - 8 - 2001.- No. 1033.

Daftar Isian 307 tgl. — No. —

UNTUK SERTIPIKAT

Takengon Tgl. 15 Pebruari 2002

Kepala Kantor Pertanahan
Kabupaten/Kotamadya
Aceh Tengah

= Drs. BUDI YAZIR .=

NIP 010172837

Takengon. Tgl. 18 - 8 - 2001.-

Kepala Seksi Pengukuran dan Pendaftaran Tanah

Kantor Pertanahan
Kabupaten/Kotamadya
Aceh Tengah

ttd

= JAMALUDDIN,SH =

NIP 010159807.-

Lihat surat ukur / gambar situasi Pemisahan / Penggabungan / Pengganti Nomor : ..... /19..... Nomor hak : .....

Dikeluarkan surat ukur/gambar situasi		Luas	Nomor hak	Sisa luas
Tanggal	Nomor			

Sisanya diuraikan dalam surat ukur / gambar situasi Nomor : ..... /19..... Nomor hak .....