Kel. Kolak I — Pemda

DAFTAR ISIAN 206

Kantor / Rumah Dinas Peternakan

BADAN PERTANAHAN NASIONAL

8. Kantor / Rumah Dinas - Peternakan.

12

SERTIPIKAT

(TANDA BUKTI HAK)

Kec.	**: Kec. Bebesen**
No. Urut	**: 12**
Alamat	: Blang Kolak II
No. Sertifikat	: 01.09.02.09.4.00009
Tahun	: 15 Februari 2002
Peruntukan	: Tanah Syariat Islam/Rumah Dinas
SKPK	**: Dinas Syariat Islam**

KANTOR PERTANAHAN

KABUPATEN/KOTAMADYA

ACEH TENGAH

.....

AL 950340

01 · 09 · 02 · 09 · 4 · 00009

BADAN PERTANAHAN NASIONAL

"S E R T I P I K A T"

BUKU TANAH

HAK : PAKAI No. 9

PROPINSI : DAERAH ISTIMEWA ACEH

KABUPATEN/KOTAMADYA : ACEH TENGAH

KECAMATAN : BEBESEN

D E S A/KELURAHAN : BLENG KOLAK II

KANTOR PERTANAHAN
KABUPATEN/KOTAMADYA

ACEH TENGAH

DAFTAR ISIAN 208
No. 30 /19 2002
DAFTAR ISIAN 307
No. ..... /19....

AL. 980340

0	1	.	0	2	.	0	9	.	0	9	.	4	.	0	0	0	0	9	

PENDAFTARAN - PERTAMA

Halaman :

a) HAK PAKAI
No. 9
Desa BLANG KOLAK II

b) NAMA JALAN/PERSIL

c) ASAL PERSIL

1. Konversi
2. Pemberian hak Pakai
3. Pemisahan
4. Penggabungan

d) SURAT KEPUTUSAN

KEPALA KANTOR WILAYAH BPN
PROV. NANGGROE ACEH DARUSSALAM
NOMOR. 4/HP/BPN/ 2002.
Tgl. 28 Januari 2002

Uang pemasukan/biaya administrasi

Lamanya hak berlaku

Selama masih dipergunakan.

Berakhirnya hak

Tgl.

e) SURAT UKUR / GAMBAR SITUASI

Tgl. 18 Agustus 2001

No. 09

Luas 12.251 M2.

f) NAMA PEMEGANG HAK

PEMERINTAH KABUPATEN ACEH TENGAH BERKEDUDUKAN DI-TAKENGON.-

g) PEMBUKUAN

Takengon Tgl. 15 Pebruari 2002

Kepala Kantor Pertanahan
Kabupaten/Kotamadya

ACEH TENGAH

ttd

=. DRS. BUDI YAZIR .=

NIP 010172837

h) PENERBITAN SERTIPIKAT

Takengon Tgl. 15 Pebruari 2002.

Kepala Kantor Pertanahan
Kabupaten/Kotamadya

ACEH TENGAH

=. DRS. BUDI YAZIR .=

NIP 010172837

i) PENUNJUK

DAFTAR ISIAN 207

01	09	02	09	4	00009

Nomor hak : 9

SURAT UKUR

NIB.01.09.02.09.00023

~~GAMBAR SITUASI~~

Nomor : 09 ~~/19~~ 2000.-

SEBIDANG TANAH TERLETAK DALAM

Propinsi : Daerah Istimewa Aceh

Kabupaten/~~Kotamadya~~ : Aceh Tengah

Kecamatan : Bebesen

Desa/~~Kelurahan~~ : Blang Kolak II

Peta : Garis

Lembar : 34.45 Kotak : A.B.5 A.B. 1 Nomor Pendaftaran : .....


Keadaan Tanah : Sebidang tanah yang diatasnya terdapat Bangunan Kantor /Rumah Dinas Perternakan Kabupaten Aceh Tengah

Tanda-tanda batas : Pagar kawat berduri.

Luas : 12.251 M2. (Dua belas ribu dua ratus lima puluh satu meter persegi)

Penunjukan dan penetapan batas : .....

PERBANDINGAN 1 : 1000.-

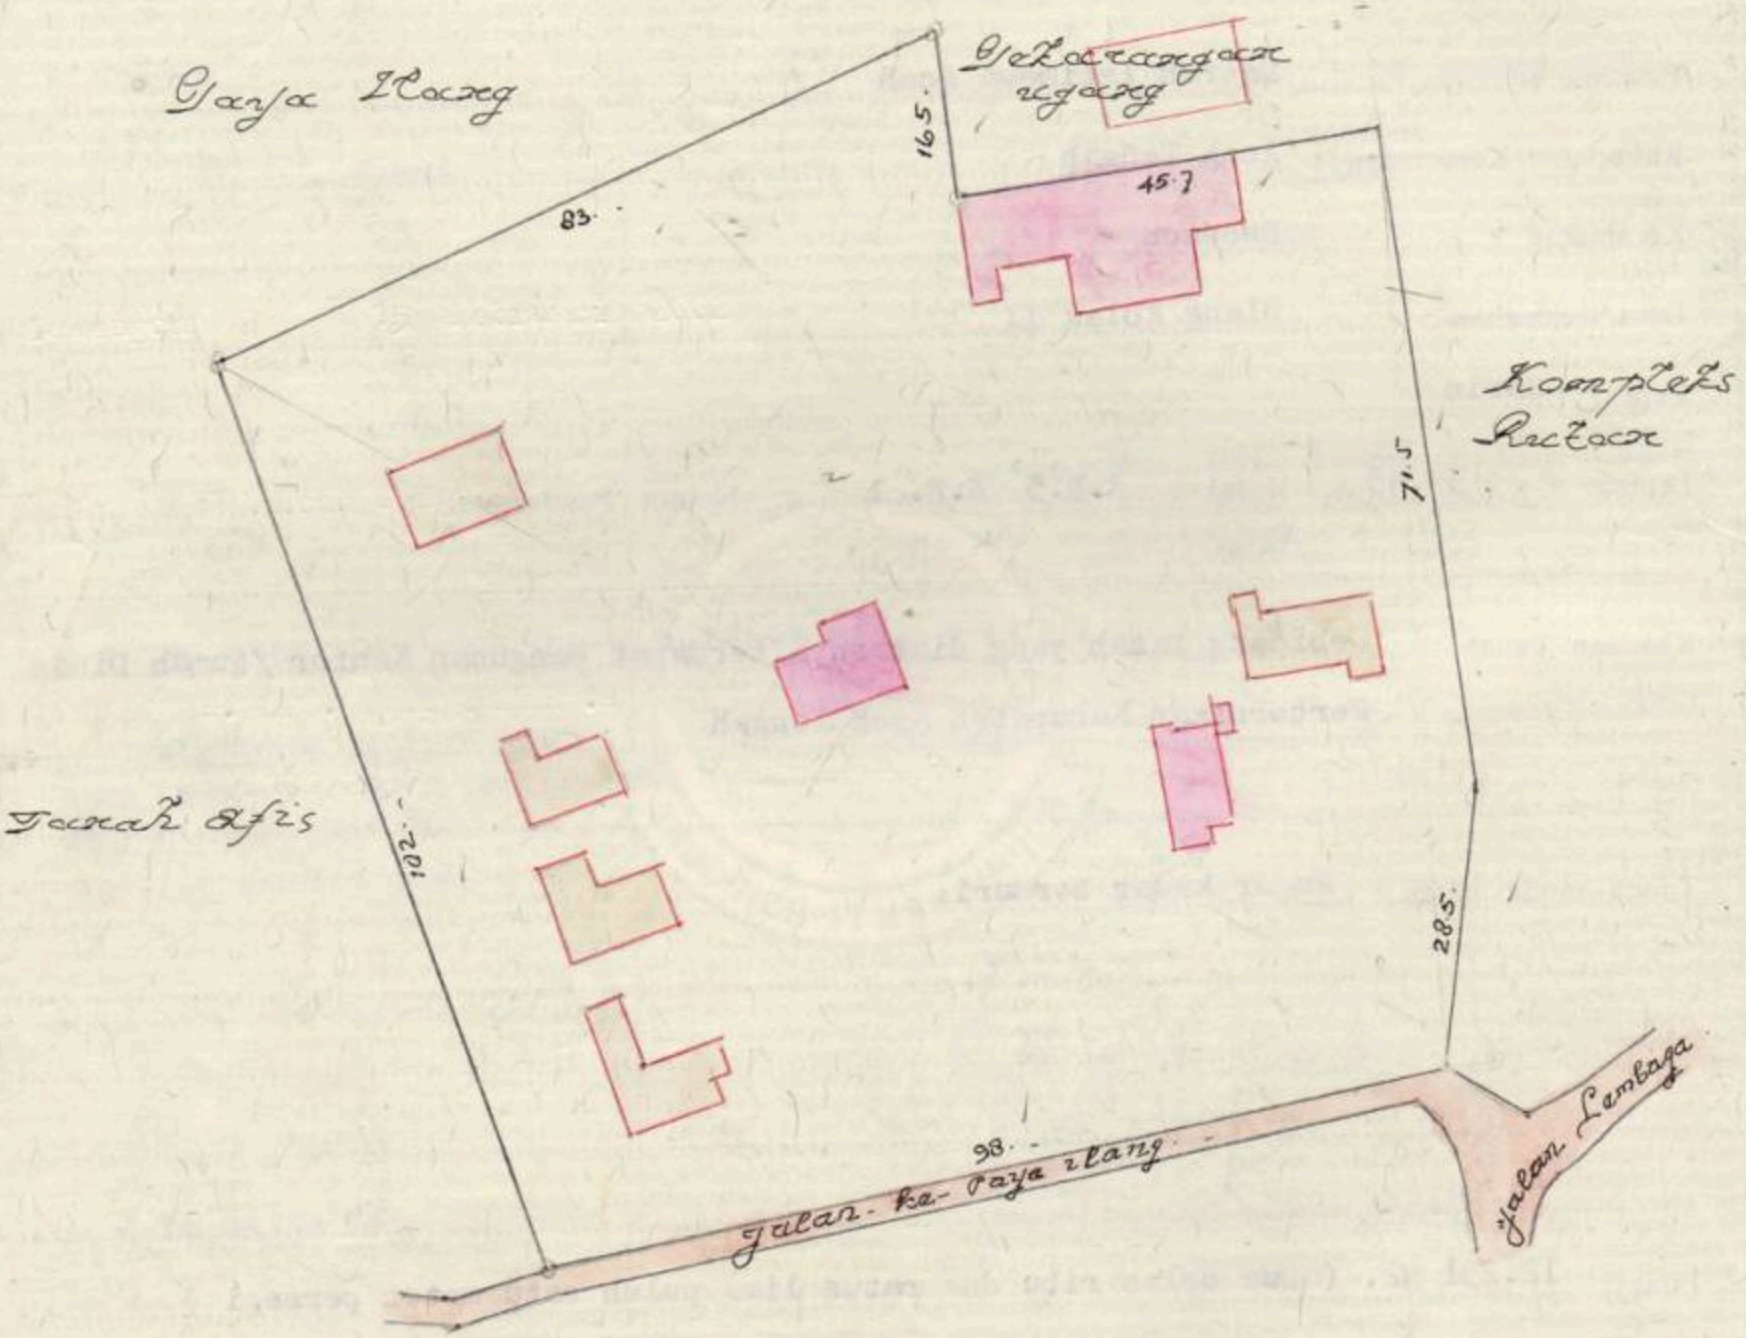

PENJELASAN : ..... batas tanah ini

Hal lain-lain : .....

.....

.....

.....

Daftar Isian 302 tgl. 8 - 8 - 2001.- No. 1033.

Daftar Isian 307 tgl. ..... No. .....

UNTUK SERTIPIKAT

Takengon Tgl. 15 Pebruari 2002

Kepala Kantor Pertanahan
Kabupaten/Kotamadya
Aceh Tengah

= DRS. BUDI YAZIR .=

NIP 010172837

Takengon. Tgl. 18 - 8 - 2001.-

Kepala Seksi Pengukuran dan Pendaftaran Tanah

Kantor Pertanahan
Kabupaten/Kotamadya
Aceh Tengah

ttd

= JAMALUDDIN,SH =

NIP 010159807.-

Lihat surat ukur / gambar situasi Pemisahan / Penggabungan / Pengganti Nomor : ..... /19..... Nomor hak : .....

Dikeluarkan surat ukur/gambar situasi		Luas	Nomor hak	Sisa luas
Tanggal	Nomor			

Sisanya diuraikan dalam surat ukur / gambar situasi Nomor : ..... /19..... Nomor hak .....