Jurusita Tk I
Blang Kolak I / Musara Alun

DAFTAR ISIAN 206

BADAN PERTANAHAN NASIONAL

9

SERTIPIKAT

(TANDA BUKTI HAK)

Kec. : Kec. Bebesen
No. Urut : 9
Alamat : Blang Kolak I
No. Sertifikat : 01.09.02.12.4.00005
Tahun : 28 September 1994
Peruntukan : Tanah Gelanggang Musara Alun
SKPK : Disbudparpora

KANTOR PERTANAHAN
KABUPATEN/~~KOTAMADYA~~
ACEH TENGAH

AD 986759

01 · 09 · 02 · 12 · 4 · 00005

BADAN PERTANAHAN NASIONAL



BUKU TANAH

PAKAI

HAK : ..... No. 6

PROPINSI : DAERAH ISTIMEWA ACEH

KABUPATEN/~~KOTAMADYA~~ : ACEH TENGAH

KECAMATAN : BEBESEN

DESA/~~KELURAHAN~~ : BLANGKOLAK I

KANTOR PERTANAHAN
KABUPATEN/~~KOTAMADYA~~

ACEH TENGAH

DAFTAR ISIAN 208
No. 1052 /1994

DAFTAR ISIAN 307
No. 3214 /1994

0	1	·	0	9	·	0	2	·	1	2	·	1	·	0	0	0	5

PENDAFTARAN - PERTAMA

Halaman : Kedua.

a) HAK PAKAI

No. 5

Desa Blang Kolak I

b) NAMA JALAN/PERSIL

c) ASAL PERSIL

1. Konversi

2. Pemberian hak

Pakai Atas Tanah Negara

3. Pemisahan

4. Penggabungan

d) SURAT KEPUTUSAN

KEPALA KANTOR WILAYAH BADAN PERTANAHAN NASIONAL PROPINSI DAERAH ISTIMEWA ACEH NO.47/HPJ/BPN/94-95 TGL.22 JULI 1994

Uang pemasukan/biaya administrasi Rp.15.000.PNBP.No.20. Tanggal 3 -09- 1994

Lamanya hak berlaku

Selama di Pakai.

Berakhirnya hak

Tgl.

e) ~~SURAT UKUR~~ / GAMBAR SITUASI

Tgl. 28-09-1994

No. 1016.

Luas 55.801 M2.

f) NAMA PEMEGANG HAK

PEMERINTAH KABUPATEN DAERAH TINGKAT II ACEH TENGAH YANG BERKEDUDUKAN DI TAKENGON.

g) PEMBUKUAN

TAKENGON, Tgl. 13-09-1994

Kepala Kantor Pertanahan

~~Kabupaten/Kotamadya~~ Aceh Tengah

Kuasa

ttd.

ZAINAL ABBAS.SH

NIP 010083877

h) PENERBITAN SERTIPIKAT

TAKENGON, Tgl. 28-09-1994

Kepala Kantor Pertanahan

~~Kabupaten/Kotamadya~~ Aceh Tengah

Kuasa

ZAINAL ABBAS.SH

NIP 010083877

i) PENUNJUK

01·09·02·12·4·00005

DAFTAR ISIAN 207

Nomor hak : 5

SURAT UKUR
GAMBAR SITUASI

Nomor : 1016 /1994

SEBIDANG TANAH TERLETAK DALAM

Propinsi : Daerah Istimewa Aceh

Kabupaten/~~Kotamadya~~ : Aceh Tengah

Kecamatan : Bebesen.

Desa/~~Kelurahan~~ : Blang Kolak I.

Peta : Peta Foto

Lembar : 45 Kotak : 20 Nomor Pendaftaran : .....


Keadaan Tanah : Berupa tanah tempat sarana Olag Raga - sarana olah raga (Gelanggang Musara Alun) (Gelanggang Musara Alun).

Tanda-tanda batas : .....

Luas : 55.601 M2 (Lima puluh lima ribu delapan ratus satu meter persegi)

Penunjukan dan penetapan batas : oleh pemohon dan Kepala Desa pada saat pengukuran di lapangan

PERBANDINGAN 1 : 2000.-

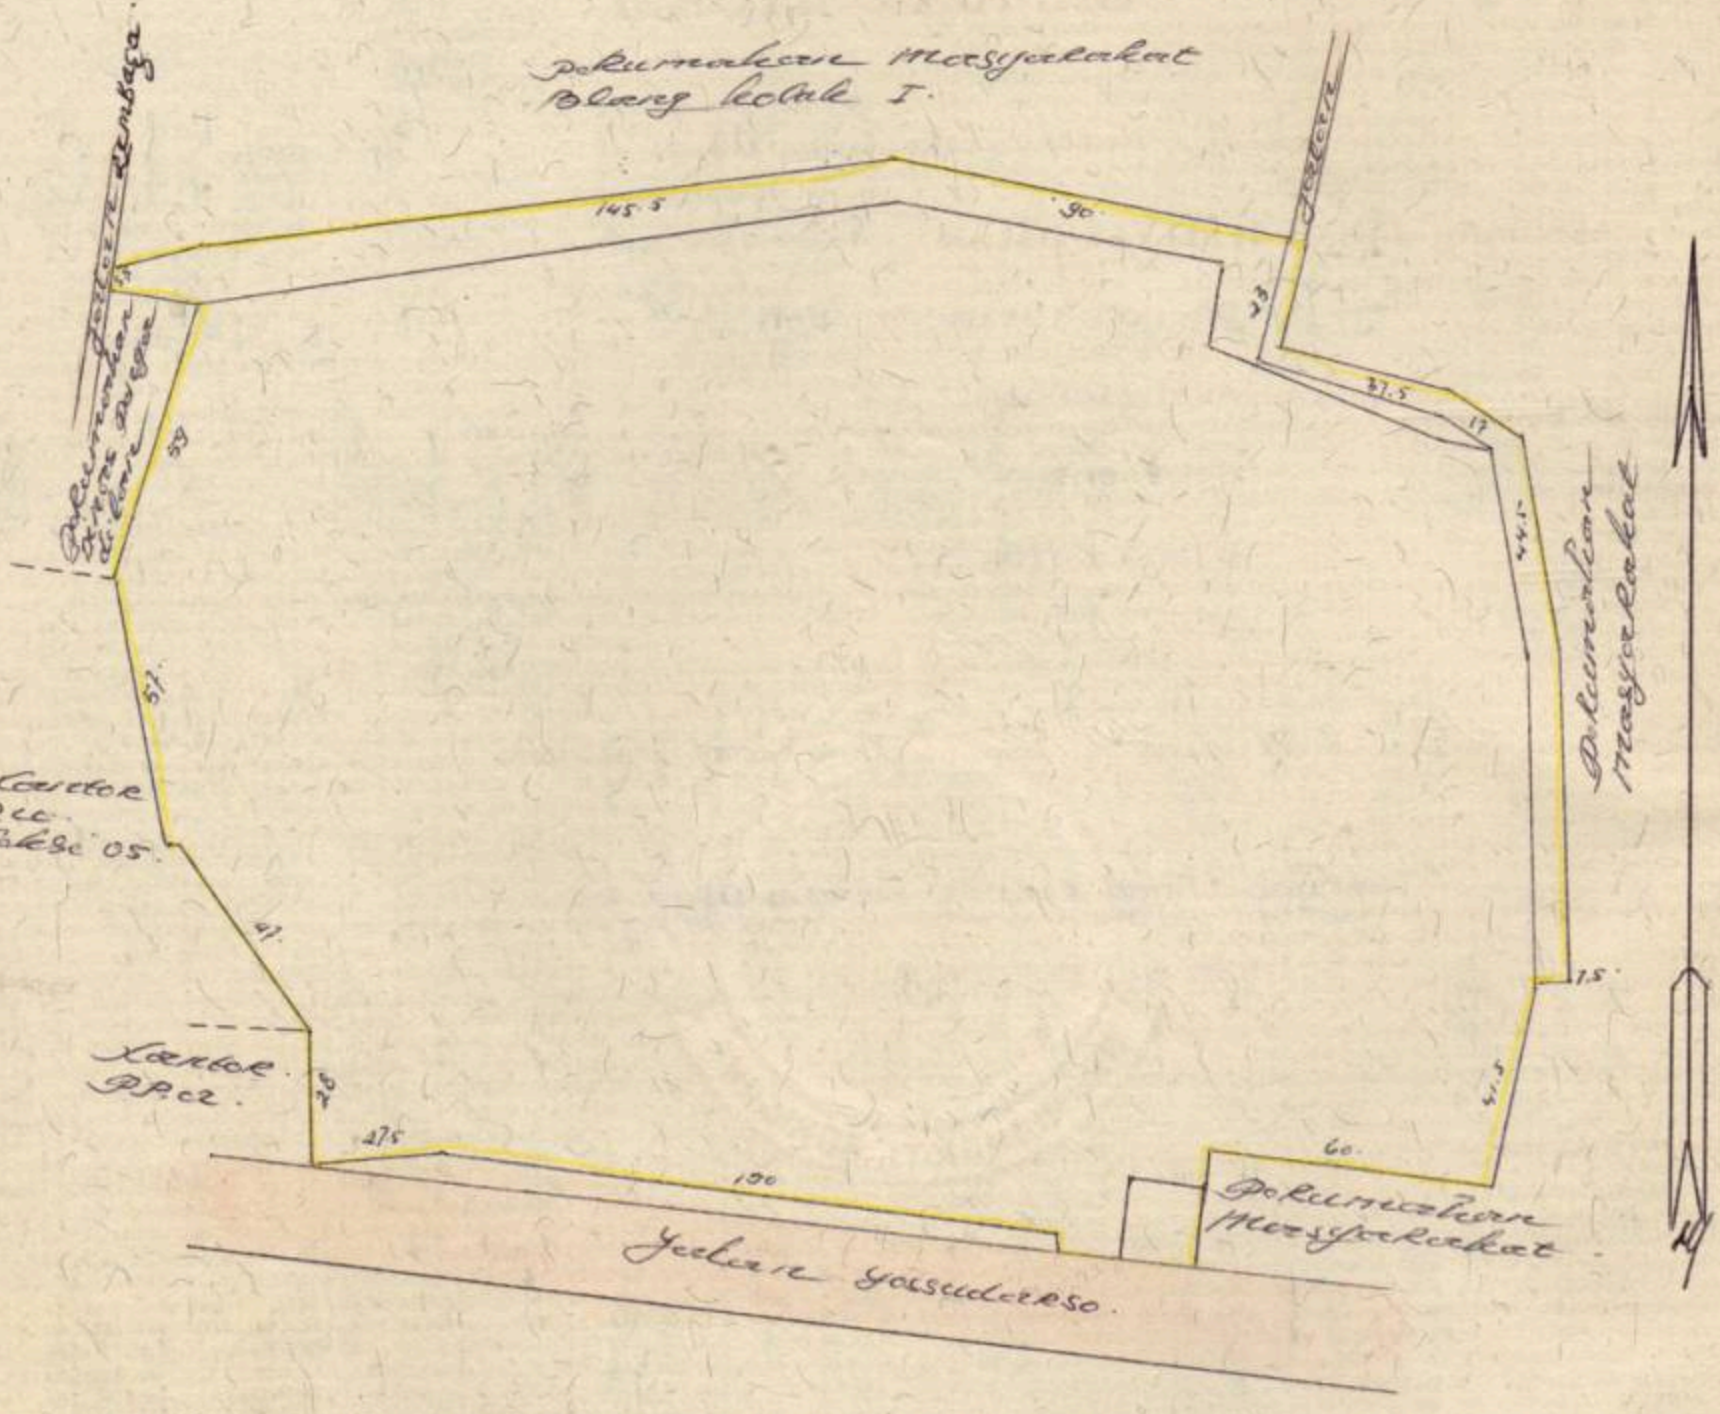

PENJELASAN : ..... batas tanah ini

Hal lain-lain : Gambar Situasi ini adalah merupakan salinan dari :

Peta Situasi NO.01.09/151/94. Tgl.11-05-1994

Daftar Isian 302 tgl. ..... No. .....

Daftar Isian 307 tgl. 28-09-1994 No. 3215.

UNTUK SERTIPIKAT

Takengon Tgl. 28-09-1994 19...

Kepala Kantor Pertanahan
Kabupaten/Kotamadya
Aceh Tengah

Kuasa

ZAINAL ABBAS.SH

NIP 010083877

Takengon Tgl. 28-09-1994 19...

Kepala Seksi Pengukuran dan Pendaftaran Tanah

Kantor Pertanahan
Kabupaten/Kotamadya
Aceh Tengah

ttd

ZAINAL ABBAS.SH

NIP 010083877

Lihat surat ukur / gambar situasi Pemisahan / Penggabungan / Pengganti Nomor : ..... /19..... Nomor hak : .....

Dikeluarkan surat ukur/gambar situasi		Luas	Nomor hak	Sisa luas
Tanggal	Nomor			

Sisanya diuraikan dalam surat ukur / gambar situasi Nomor : ..... /19..... Nomor hak .....