BADAN PERTANAHAN NASIONAL

BUKU TANAH

HAK : PAKAI. No. 37

PROPINSI : DAERAH ISTIMEWA ACEH.

KABUPATEN/~~KOTAMADYA~~ : ACEH TENGAH.

KECAMATAN : KOTA TAKENGON.

D E S A/KELURAHAN : TAKENGON BARAT.

KANTOR PERTANAHAN
KABUPATEN/~~KOTAMADYA~~
ACEH TENGAH.

DAFTAR ISIAN 208
No. 1373 /1994

DAFTAR ISIAN 307
No. 3909 /1994

0	1	·	0	9	·	0	1	·	1	0	·	4	·	0	0	3	7

PENDAFTARAN - PERTAMA

Halaman : Kedua.

a) HAK : PAKAI.

No. : 37

Desa : Takengon Barat.

b) NAMA JALAN/PERSIL

c) ASAL PERSIL

1. ~~Konversi~~

2. Pemberian hak Pakai.

3. ~~Pemisahan~~

4. ~~Penggabungan~~

d) SURAT KEPUTUSAN

KEPALA KANTOR WILAYAH BADAN-PERTANAHAN NASIONAL PROPINSI DAERAH ISTIMEWA ACEH.
NOMOR :71/HPJ/BPN/1994-1995.
TANGGAL, 1 SEPTEMBER 1994.

Uang pemasukan/biaya administrasi
Rp.15.000,- PNBP. No.2.
Tanggal, 12 Desember 1994.

Lamanya hak berlaku
Selama di Pakai.
Berakhirnya hak
Tgl.

e) ~~SURAT UKUR~~
GAMBAR SITUASI

Tgl. 12-12-1994.

No. 1332.

Luas 22.841 M2.-

f) NAMA PEMEGANG HAK

=.PEMERINTAH KABUPATEN DAERAH TK.II ACEH TENGAH
YANG BERKEDUDUKAN DI TAKENGON.=

g) PEMBUKUAN

Takengon Tgl. 12 Desember 1994.

Kepala Kantor Pertanahan
Kabupaten/~~Kotamadya~~
Aceh Tengah

Kuasa,

ttd.

=. ZAINAL ABBAS.SH .=

NIP 010083877.

h) PENERBITAN SERTIPIKAT

Takengon Tgl. 12 Desember 1994.

Kepala Kantor Pertanahan
Kabupaten/~~Kotamadya~~
Aceh Tengah

Kuasa

=. ZAINAL ABBAS.SH .=

NIP 010083877.

i) PENUNJUK

01	09	01	10	4	00037

DAFTAR ISIAN 207

37

Nomor hak : .....

SURAT UKUR
GAMBAR SITUASI

Nomor : 1332 /1994

SEBIDANG TANAH TERLETAK DALAM

Propinsi : : Daerah Istimewa Aceh.

Kabupaten/~~Kotamadya~~ : Aceh Tengah.

Kecamatan : : Kota Takengon.

Desa/Kelurahan : : Takengon Barat.

Peta : : Peta Foto

Lembar : 46 Kotak : B-4 Nomor Pendaftaran : .....


Keadaan Tanah : : Sebidang tanah yang diatasnya terdapat bangunan Pemda.
(Kantor Bupati dan Kantor DPR.)

Tanda-tanda batas : .....


Luas : 22.841 M2. (Dua puluh dua ribu delapan ratus empat puluh satu meter persegi)


Penunjukan dan penetapan batas : oleh Pemohon dan Kepala Desa/Lurah.

PERBANDINGAN 1 : 1000.-

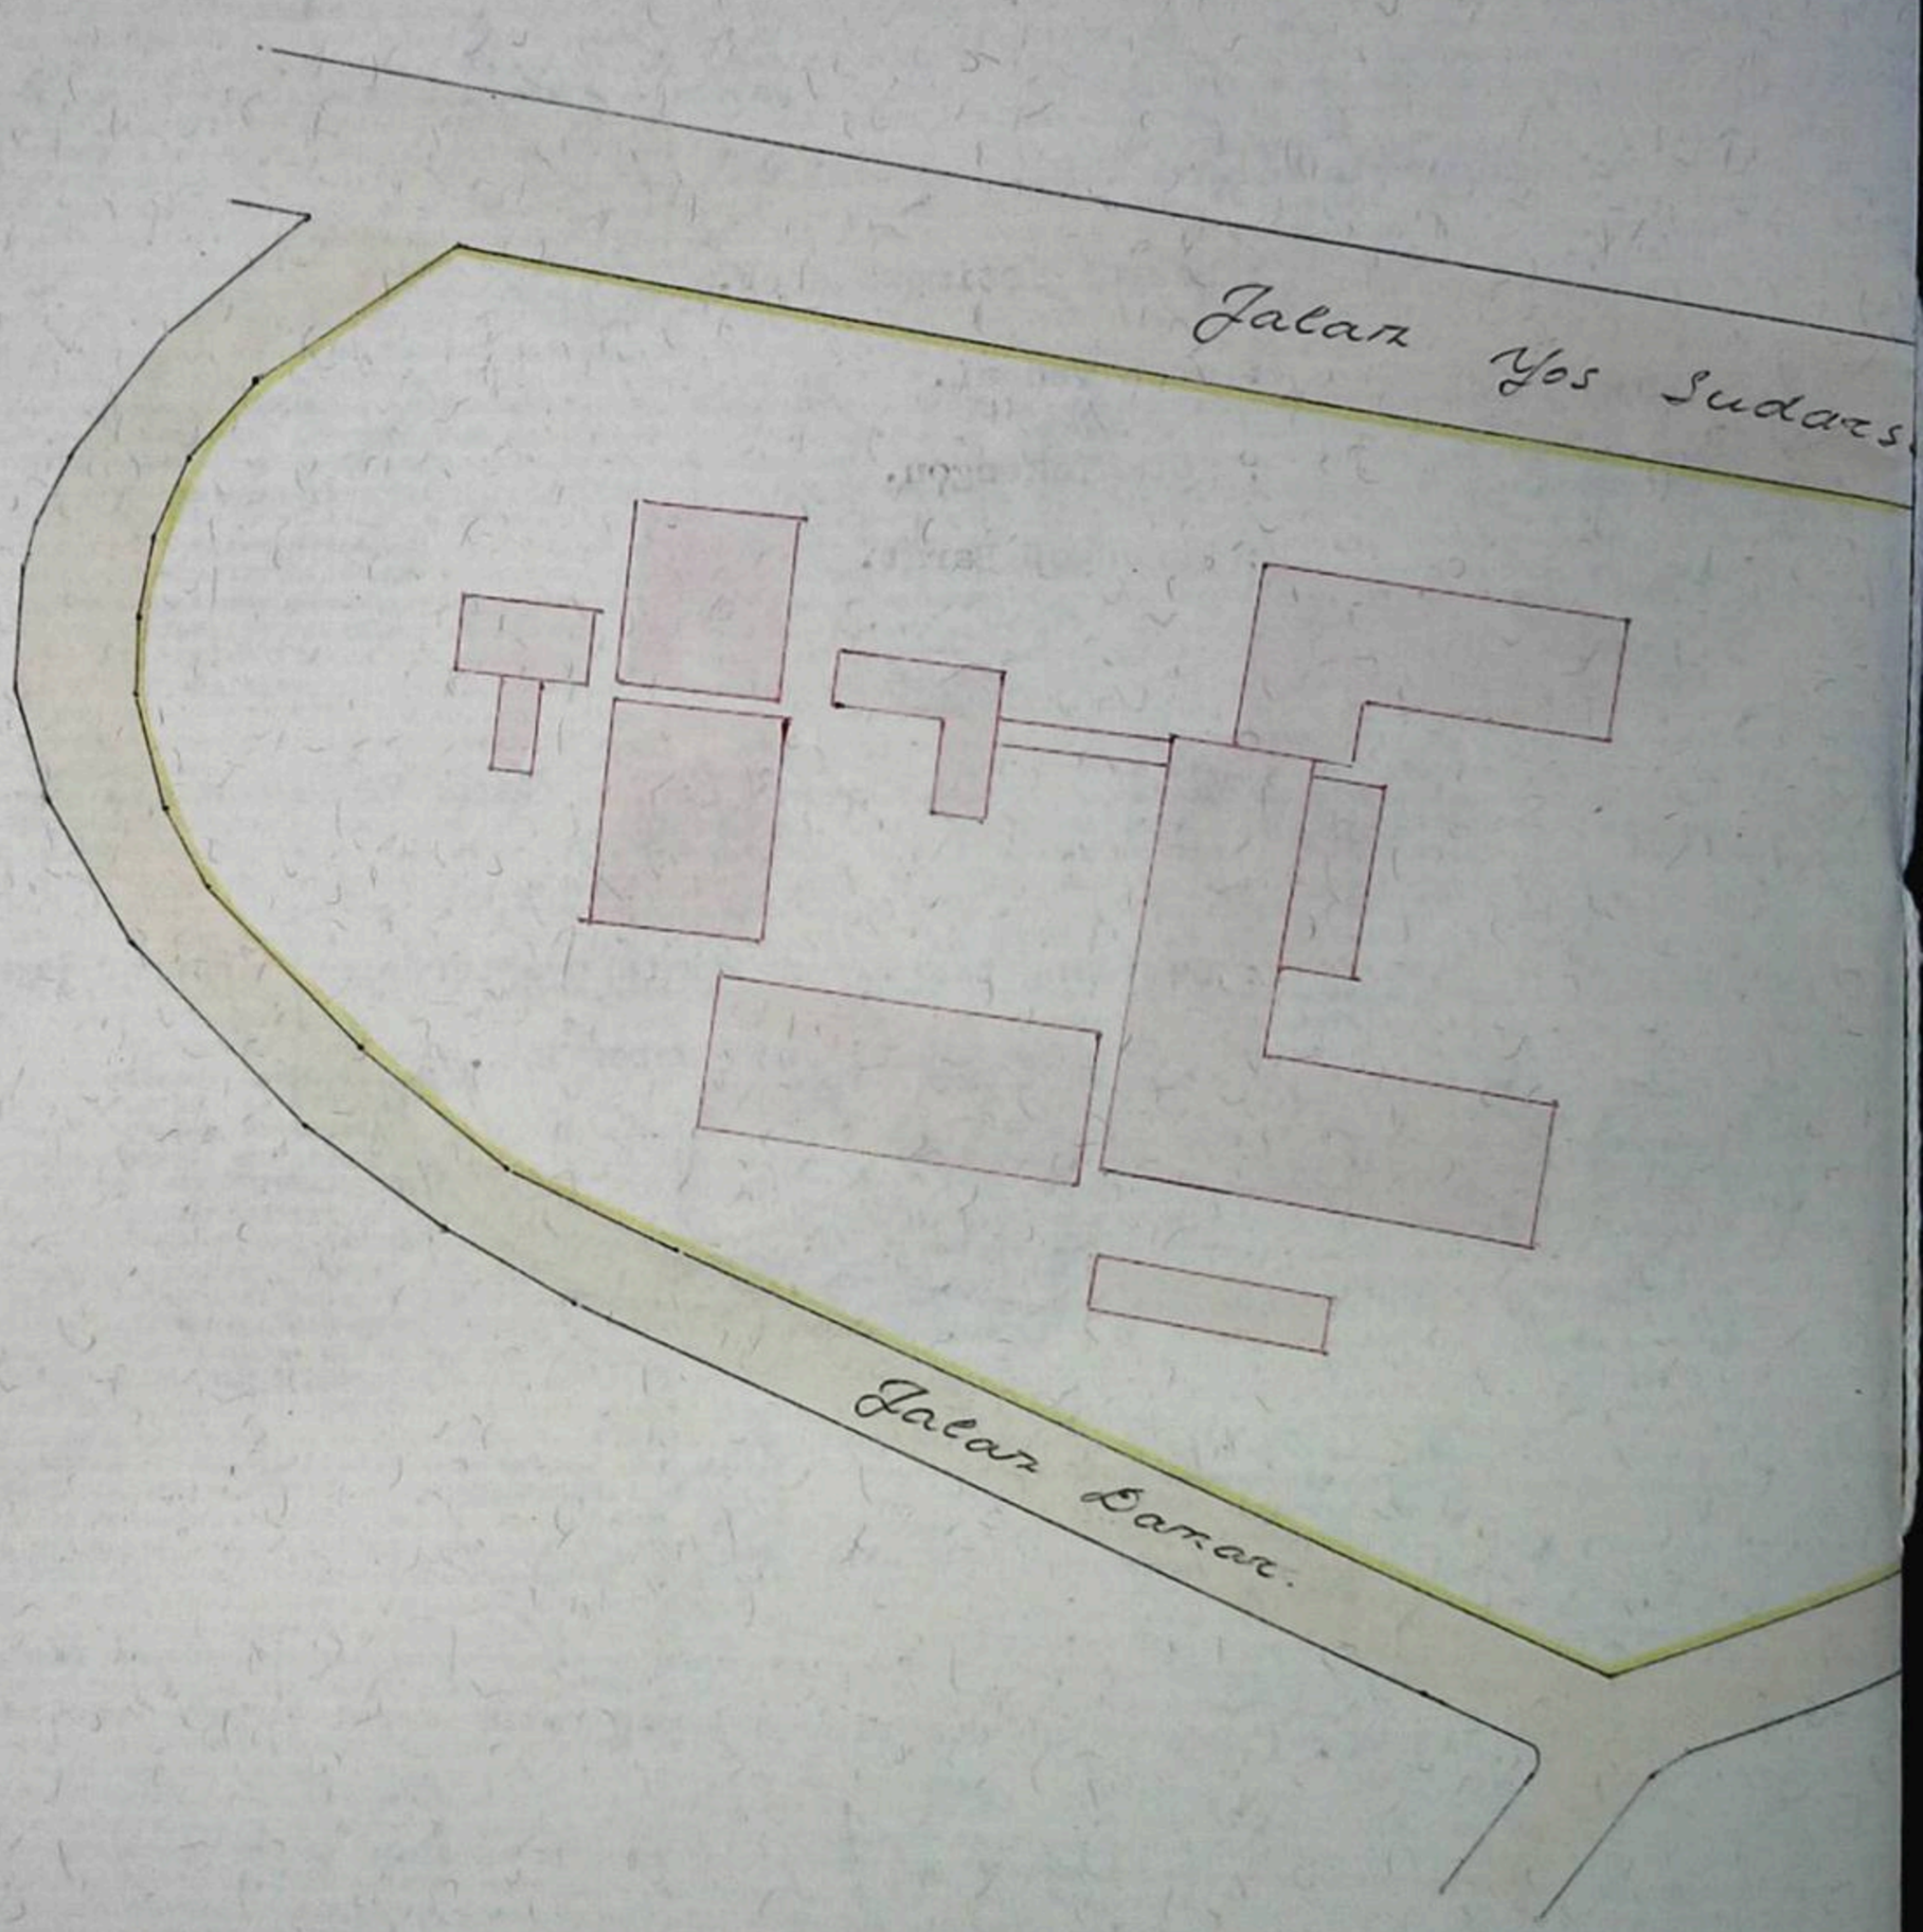

PENJELASAN : ..... batas tanah ini

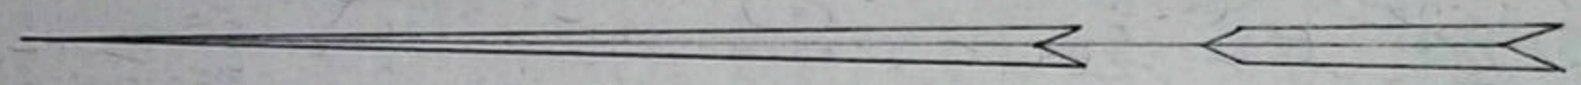

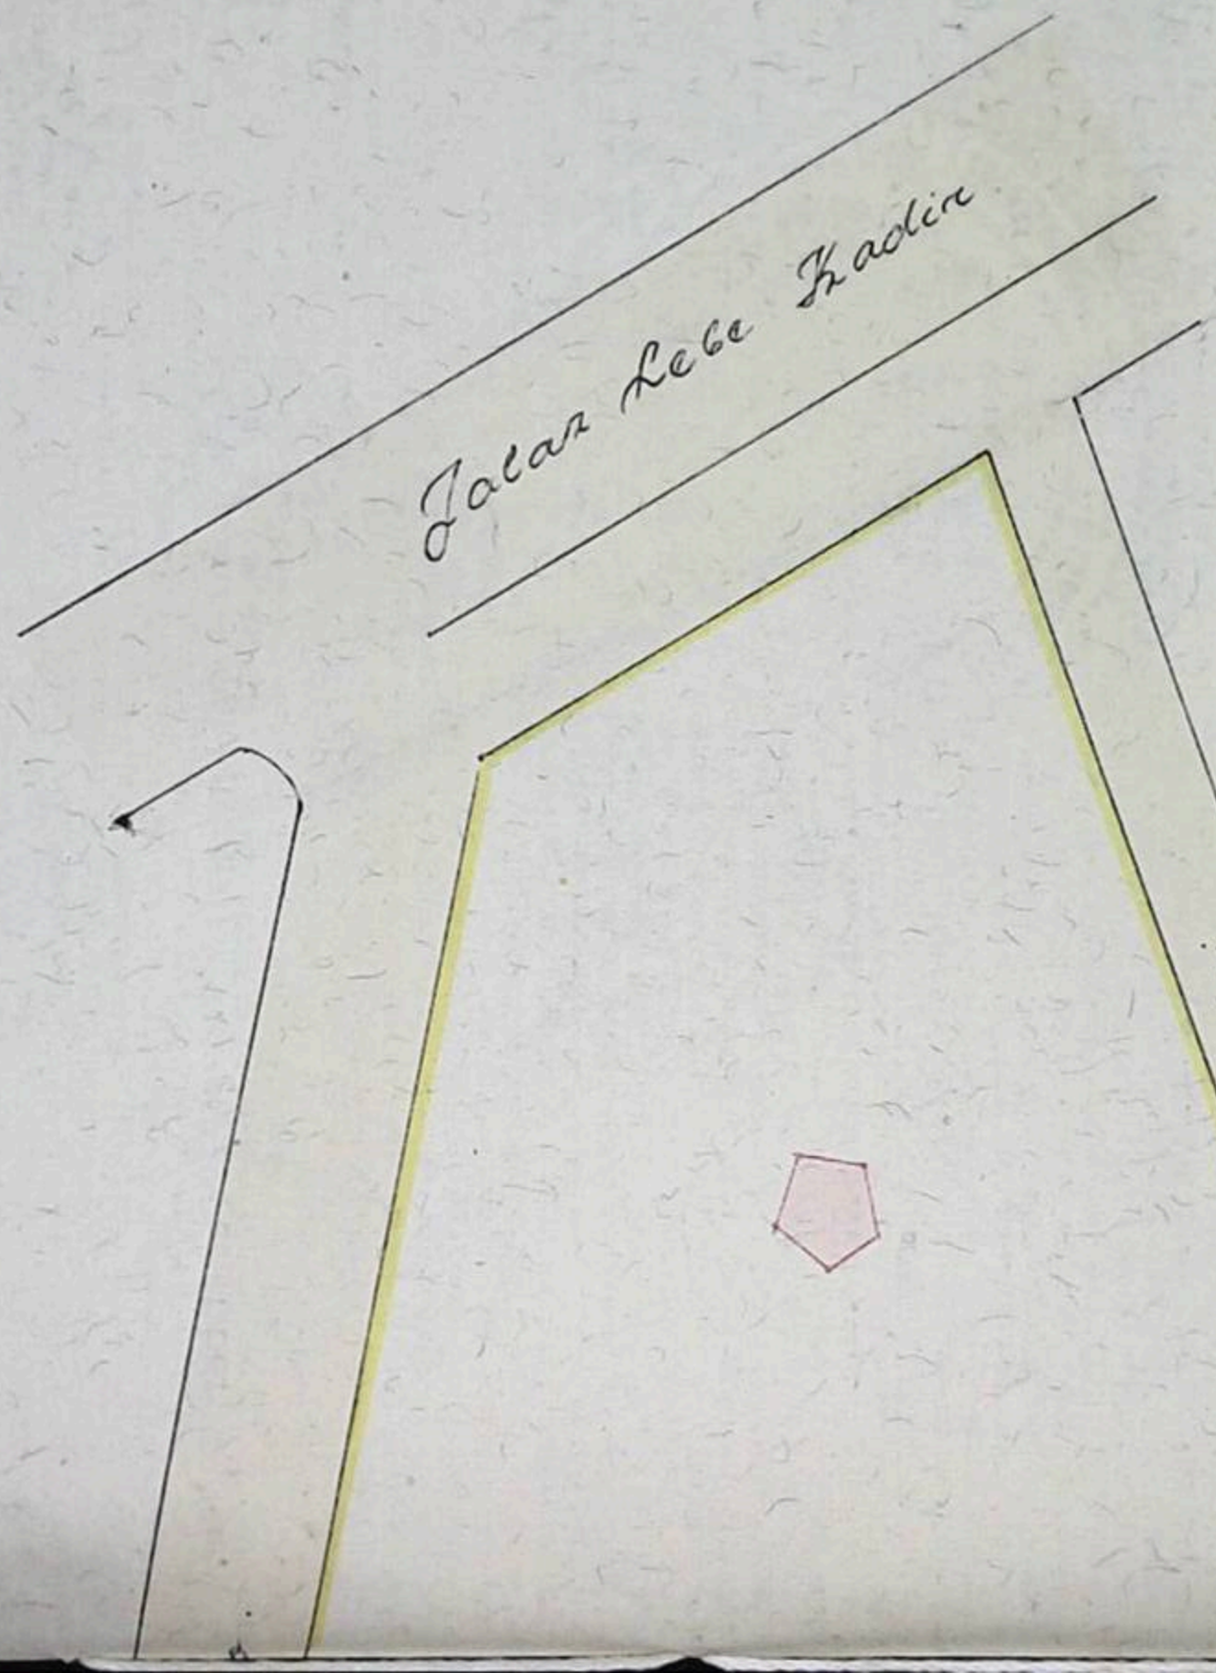
Jalan Lebe Kadir
Jalan Kenari

Hal lain-lain : Gambar Situasi ini adalah merupakan Petikan dari Peta Situasi No.01.09/ 144/1994. tgl.11-5-1994.

Daftar Isian 302 tgl. ..... No. .....

Daftar Isian 307 tgl. 12 - 12 - 1994. No. 3990

UNTUK SERTIPIKAT

Takengon Tgl. 12 Desember 19 94.

Kepala Kantor Pertanahan
Kabupaten/~~Kotamadya~~
Aceh Tengah

Kuasa,

=. ZAINAL ABBAS.SH .=

NIP 010083877.

Takengon Tgl. 12 Desember 19 94.

Kepala Seksi Pengukuran dan Pendaftaran Tanah
Kantor Pertanahan
Kabupaten/~~Kotamadya~~
Aceh Tengah

Ttd.

=. ZAINAL ABBAS.SH .=

NIP 010083877.

Lihat surat ukur / gambar situasi Pemisahan / Penggabungan / Pengganti Nomor : ..... /19..... Nomor hak : .....

Dikeluarkan surat ukur/gambar situasi		Luas	Nomor hak	Sisa luas
Tanggal	Nomor			

Sisanya diuraikan dalam surat ukur / gambar situasi Nomor : ..... /19..... Nomor hak .....