BADAN PERTANAHAN NASIONAL



BUKU TANAH

HAK : PAKAI. No. 38

PROPINSI : DAERAH ISTIMEWA ACEH.

KABUPATEN/KOTAMADYA : ACEH TENGAH.

KECAMATAN : KOTA TAKENGON.

D E S A/KELURAHAN : TAKENGON BARAT.

KANTOR PERTANAHAN
KABUPATEN/KOTAMADYA

ACEH TENGAH.

DAFTAR ISIAN 208
No. 1374 /1994

DAFTAR ISIAN 307
No. 3991 /1994

0	1	.	0	9	.	0	1	.	1	0	.	4	.	0	0	0	3	8

PENDAFTARAN - PERTAMA

Halaman : Kedua.

a) HAK : PAKAI.

No. : 38

Desa

b) NAMA JALAN/PERSIL

c) ASAL PERSIL

1. ~~Konversi~~
2. Pemberian hak Pakai.
3. ~~Pemisahan~~
4. ~~Penggabungan~~

d) SURAT KEPUTUSAN

KEPALA KANTOR WILAYAH BADAN-PERTANAHAN NASIONAL PROPINSI DAERAH ISTIMEWA ACEH.
NOMOR :71/HPJ/BPN/1994-1995.
TANGGAL, 1 SEPTEMBER 1994.

Uang pemasukan/biaya administrasi
Rp.15.000,- PNBP. No.2.
Tanggal, 12 Desember 1994.

Lamanya hak berlaku
Selama di Pakai.
Berakhirnya hak
Tgl.

e) ~~SURAT UKUR~~ / GAMBAR SITUASI

Tgl. 12-12-1994.
No. 1333.
Luas 8.790 M2.-

f) NAMA PEMEGANG HAK

=.PEMERINTAH KABUPATEN DAERAH TK.II ACEH TENGAH
YANG BERKEDUDUKAN DI TAKENGON.=

g) PEMBUKUAN

Takengon Tgl. 12 Desember 1994.

Kepala Kantor Pertanahan
~~Kabupaten~~/~~Kotamadya~~
Aceh Tengah

Kuasa,

ttd.

=. ZAINAL ABBAS.SH .=

NIP 010083877.

h) PENERBITAN SERTIPIKAT

Takengon Tgl. 12 Desember 1994.

Kepala Kantor Pertanahan
~~Kabupaten~~/~~Kotamadya~~
Aceh Tengah

Kuasa,

=. ZAINAL ABBAS.SH .=

NIP 010083877.

i) PENUNJUK

01	09	01	10	4	00038

DAFTAR ISIAN 207

38

Nomor hak : .....

~~SURAT UKUR~~

GAMBAR SITUASI

Nomor : 1333 /1994

SEBIDANG TANAH TERLETAK DALAM

Propinsi : Daerah Istimewa Aceh.

Kabupaten/~~Kotamadya~~ : Aceh Tengah.

Kecamatan : Kota Takengon.

Desa/Kelurahan : Takengon Barat.

Peta : Peta Garis

Lembar : 57 Kotak : C.2 Nomor Pendaftaran : .....


Keadaan Tanah : Sebidang tanah yang diatasnya terdapat bangunan Pendopo.

Tanda-tanda batas : .....

Luas : 8.790 M2. (Delapan ribu tujuh ratus sembilan puluh meter persegi)

Penunjukan dan penetapan batas : oleh Pemohon dan Kepala Desa.

PERBANDINGAN 1 : 1000

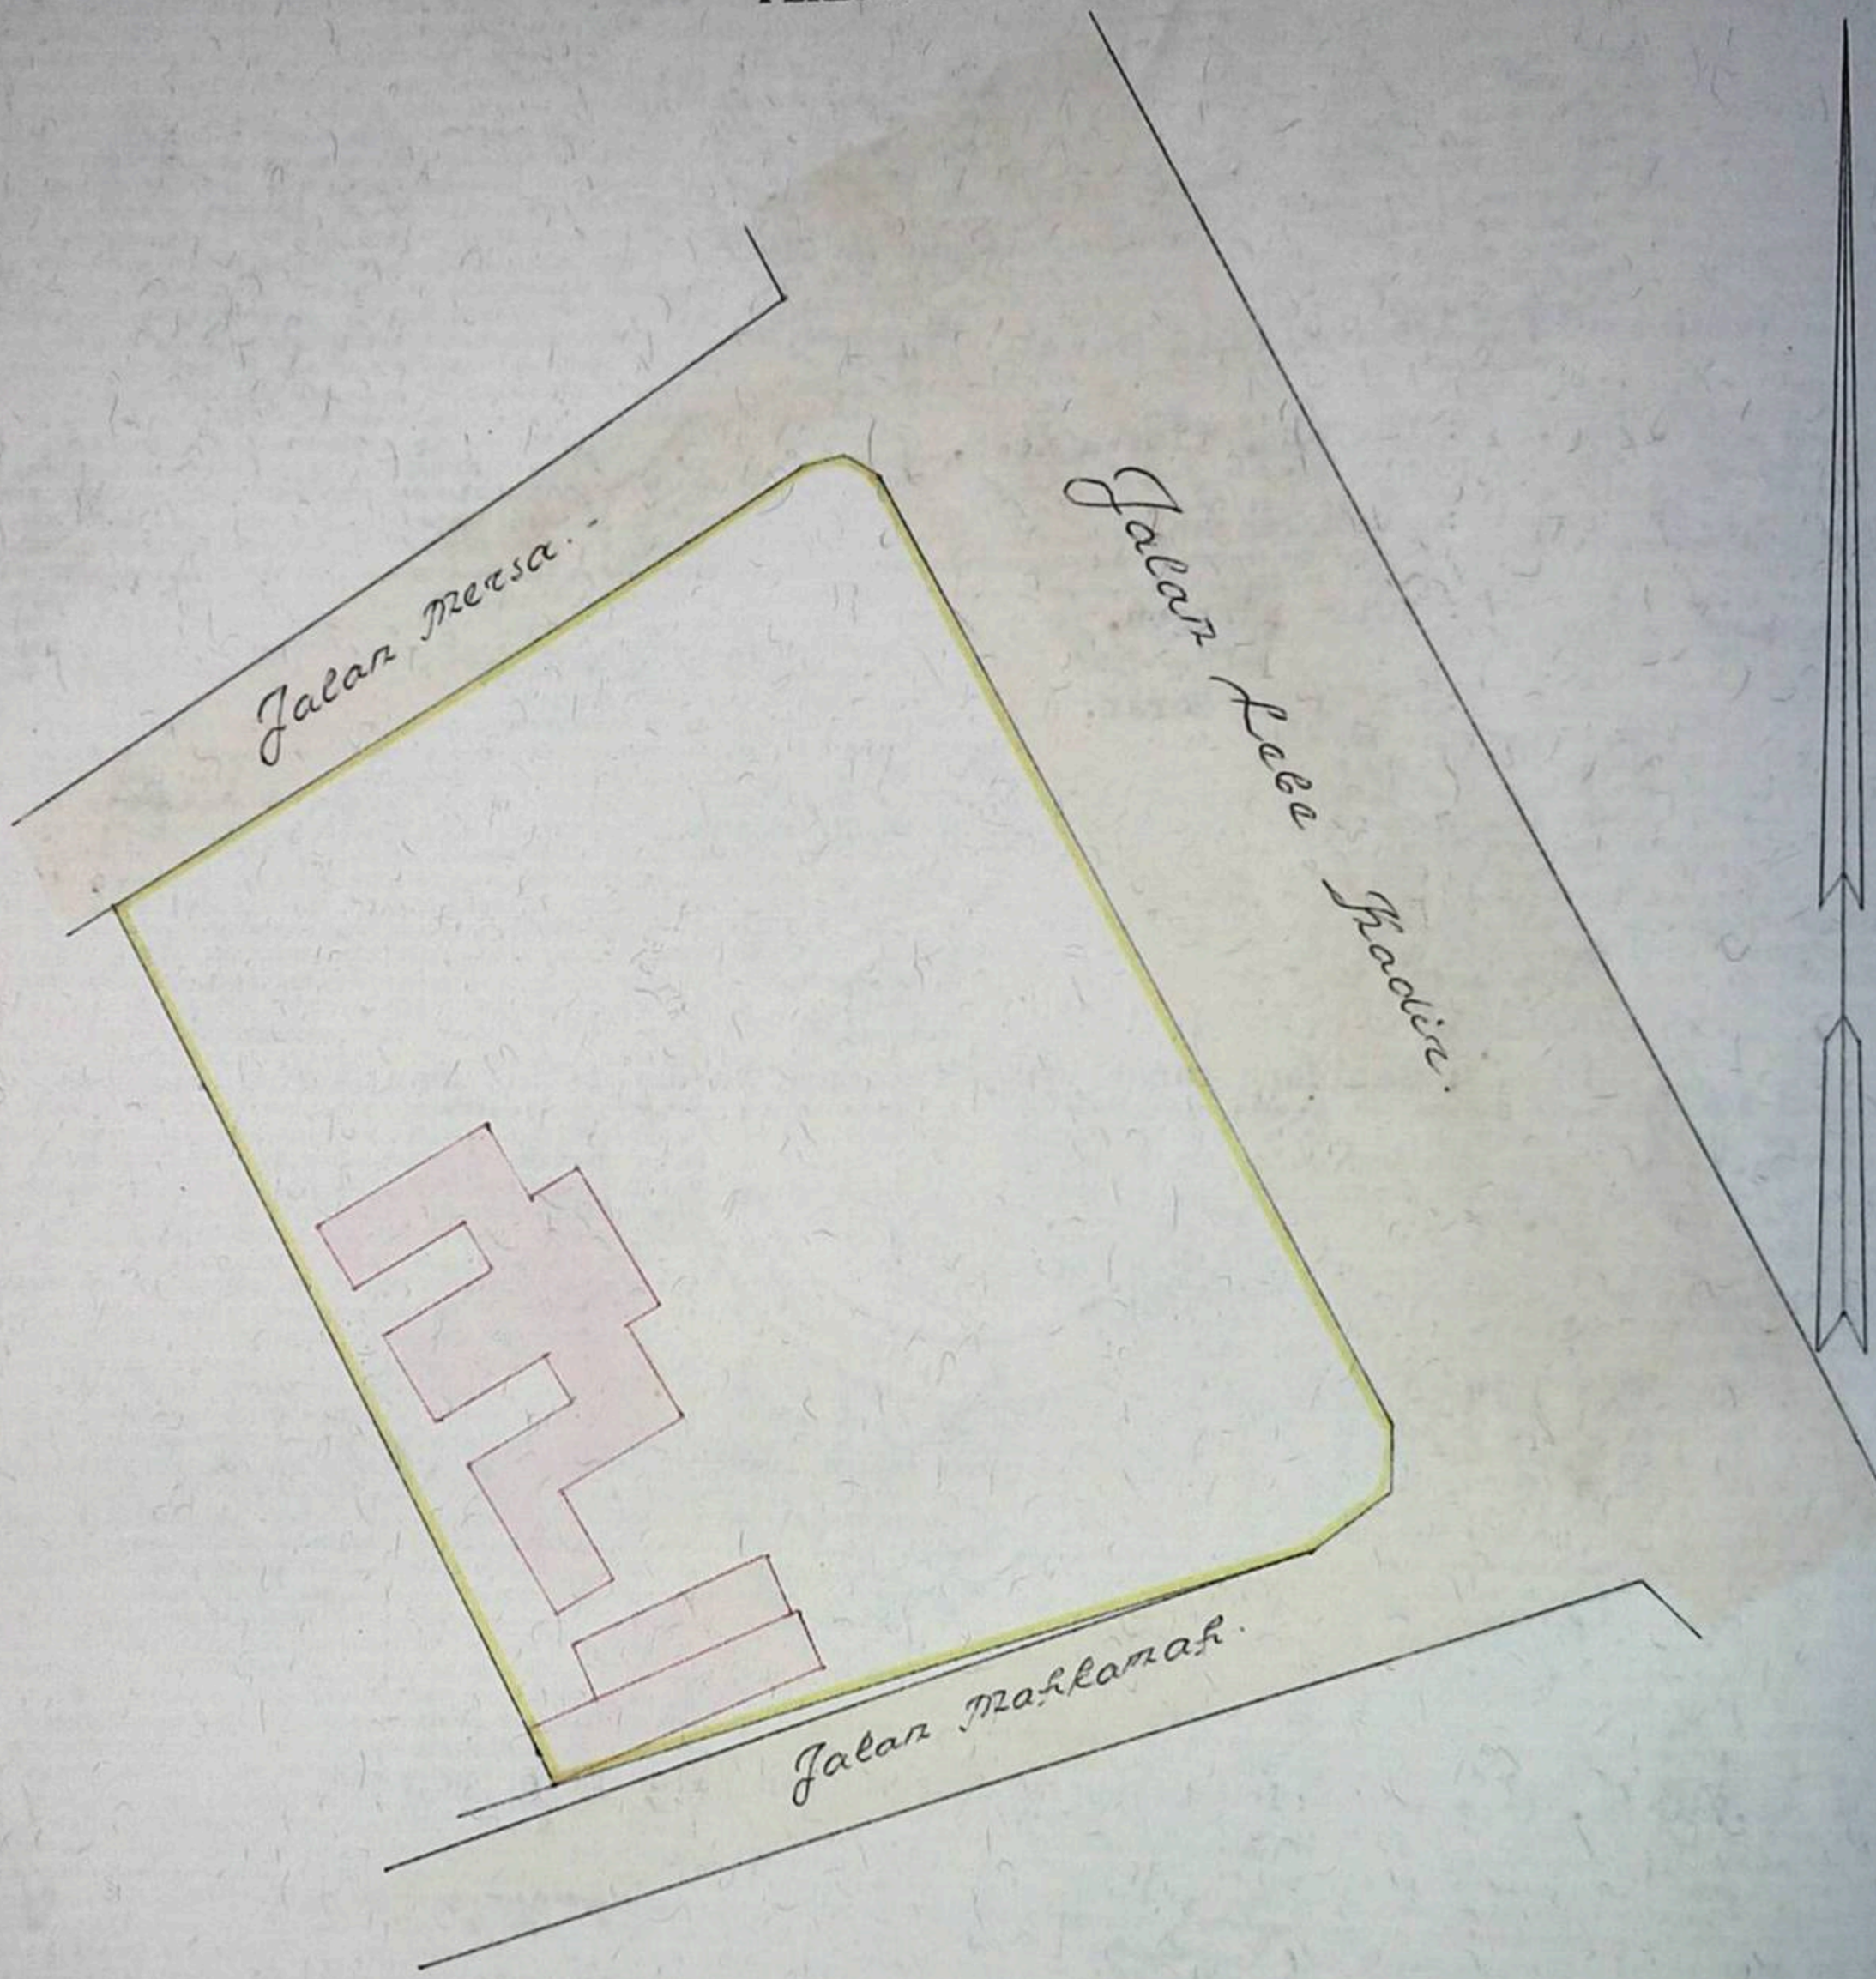

PENJELASAN : ..... **batas tanah ini**

Hal lain-lain : Gambar Situasi ini adalah merupakan Petikan dari Peta Situasi No.01.09/ 145/1994. tgl.11-5-1994.

Daftar Isian 302 tgl. 12 - 12 - 1994. No. 3992.

Daftar Isian 307 tgl. ..... No. .....

UNTUK SERTIPIKAT

Takengon Tgl. 12 Desember 1994.

Kepala Kantor Pertanahan
Kabupaten/~~Kotamadya~~
Aceh Tengah

Kuasa,

=. ZAINAL ABBAS.SH .=

NIP 010083877.

Takengon Tgl. 12 Desember 1994.

Kepala Seksi Pengukuran dan Pendaftaran Tanah

Kantor Pertanahan
Kabupaten/~~Kotamadya~~
Aceh Tengah

ttd.

=. ZAINAL ABBAS.SH .=

NIP 010083877.

Lihat surat ukur / gambar situasi — Pemisahan / Penggabungan / Pengganti Nomor : ...../19..... Nomor hak : .....

Dikeluarkan surat ukur/gambar situasi		Luas	Nomor hak	Sisa luas
Tanggal	Nomor			

Sisanya diuraikan dalam surat ukur / gambar situasi Nomor : ...../19..... Nomor hak .....