AW 753906

DAFTAR ISIAN 206

BADAN PERTANAHAN NASIONAL

17

SERTIPIKAT

(TANDA BUKTI HAK)

Kec.	: Kec. Bebesen
No. Urut	: 17
Alamat	: Kemili
No. Sertifikat	: 01.09.02.07.4.00006
Tahun	: 28 Mei 2005
Peruntukan (Rumah Adat)	: Tanah Mess Time Ruang
SKPK	: Dinas Pariwisata

KANTOR PERTANAHAN
KABUPATEN / ~~KOTAMADYA~~
ACEH TENGAH

01 • 09 • 02 • 07 • 4 • 00006

AW 753906

DAFTAR ISIAN 206

BADAN PERTANAHAN NASIONAL

SERTIPIKAT

HAK : HAKAI No. 6

PROPINSI : NANGGROE ACEH DARUSSALAM

KABUPATEN / ~~KOTAMADYA~~ : ACEH TENGAH

KECAMATAN : BEBESEN

DESA / ~~KELURAHAN~~ : KEMILI

DAFTAR ISIAN 307
No. ..... /200.....
DAFTAR ISIAN 208
No. 560. /2005

KANTOR PERTANAHAN
KABUPATEN / ~~KOTAMADYA~~
ACEH TENGAH

01 • 09 • 02 • 07 • A • 00006

Halaman :

PENDAFTARAN - PERTAMA

a) HAK : : PAKAI

No. : : 6

Desa / Kel. : Kemili

Tgl. berakhirnya hak : selama dipergunakan.

b) NIB 01.09.02.07.00136

Letak Tanah

c) ASAL HAK

1. ~~Konversi~~

2. Pemberian hak pakai

3. ~~Pemecahan / Pemisahan / Penggabungan bidang~~

d) DASAR PENDAFTARAN

1. Daftar Isian 202

Tgl.

No.

2. Surat Keputusan

Tgl. 30-04-2005

No. 7/HP/BPN/2005

3. Permohonan Pemecahan / Pemisahan / Penggabungan bidang

Tgl.

No.

e) SURAT UKUR

Tgl. 28-05-2005.

No. 33.

Luas. 7.267 M2.

f) NAMA PEMEGANG HAK

" PEMERINTAH KABUPATEN ACEH TENGAH "

berkedudukan di- TAKENGON.

Tanggal lahir / akta pendirian

g) PEMBUKUAN

Takengon , Tgl. 13-05-2005

Kepala Kantor Pertanahan

Kabupaten / ~~Kotamadya~~

Aceh Tengah

ttd.

=. DRS.BUDI YAZIR .=

NIP 010172837

h) PENERBITAN SERTIPIKAT

Takengon , Tgl. 28-05-2005

Kepala Kantor Pertanahan

Kabupaten / ~~Kotamadya~~

Aceh Tengah

=. DRS.BUDI YAZIR .=

NIP 010172837

i) PENUNJUK

DAFTAR ISIAN 207

01	•	09	•	02	•	07	•	4	•	00006

NIB : 01.09.02.07.00136

SURAT UKUR

Nomor : ....33..../ 200.5...

SEBIDANG TANAH TERLETAK DALAM

Propinsi : : Nanggroe Aceh Darussalam

Kabupaten / ~~Kotamadya~~ : : Aceh Tengah

Kecamatan : : Bebesen

Desa / ~~Kelurahan~~ : : Kemili

Peta : ..... Nomor Peta Pendaftaran : .....

Lembar : ..... Kotak : .....

.....

Keadaan Tanah : : Tempat bangunan Mess Time-Ruang / Rumah Adat Gayo

.....

.....

Tanda-tanda batas : .....

.....

.....

.....

.....

.....

Luas : 7.267 M2 (Tujuh ribu dua ratus enam puluh tujuh meter persegi)

.....

.....


.....

Penunjukan dan penetapan batas : oleh Pemohon dan Kepala Desa

.....

.....

SKALA 1 : 1000

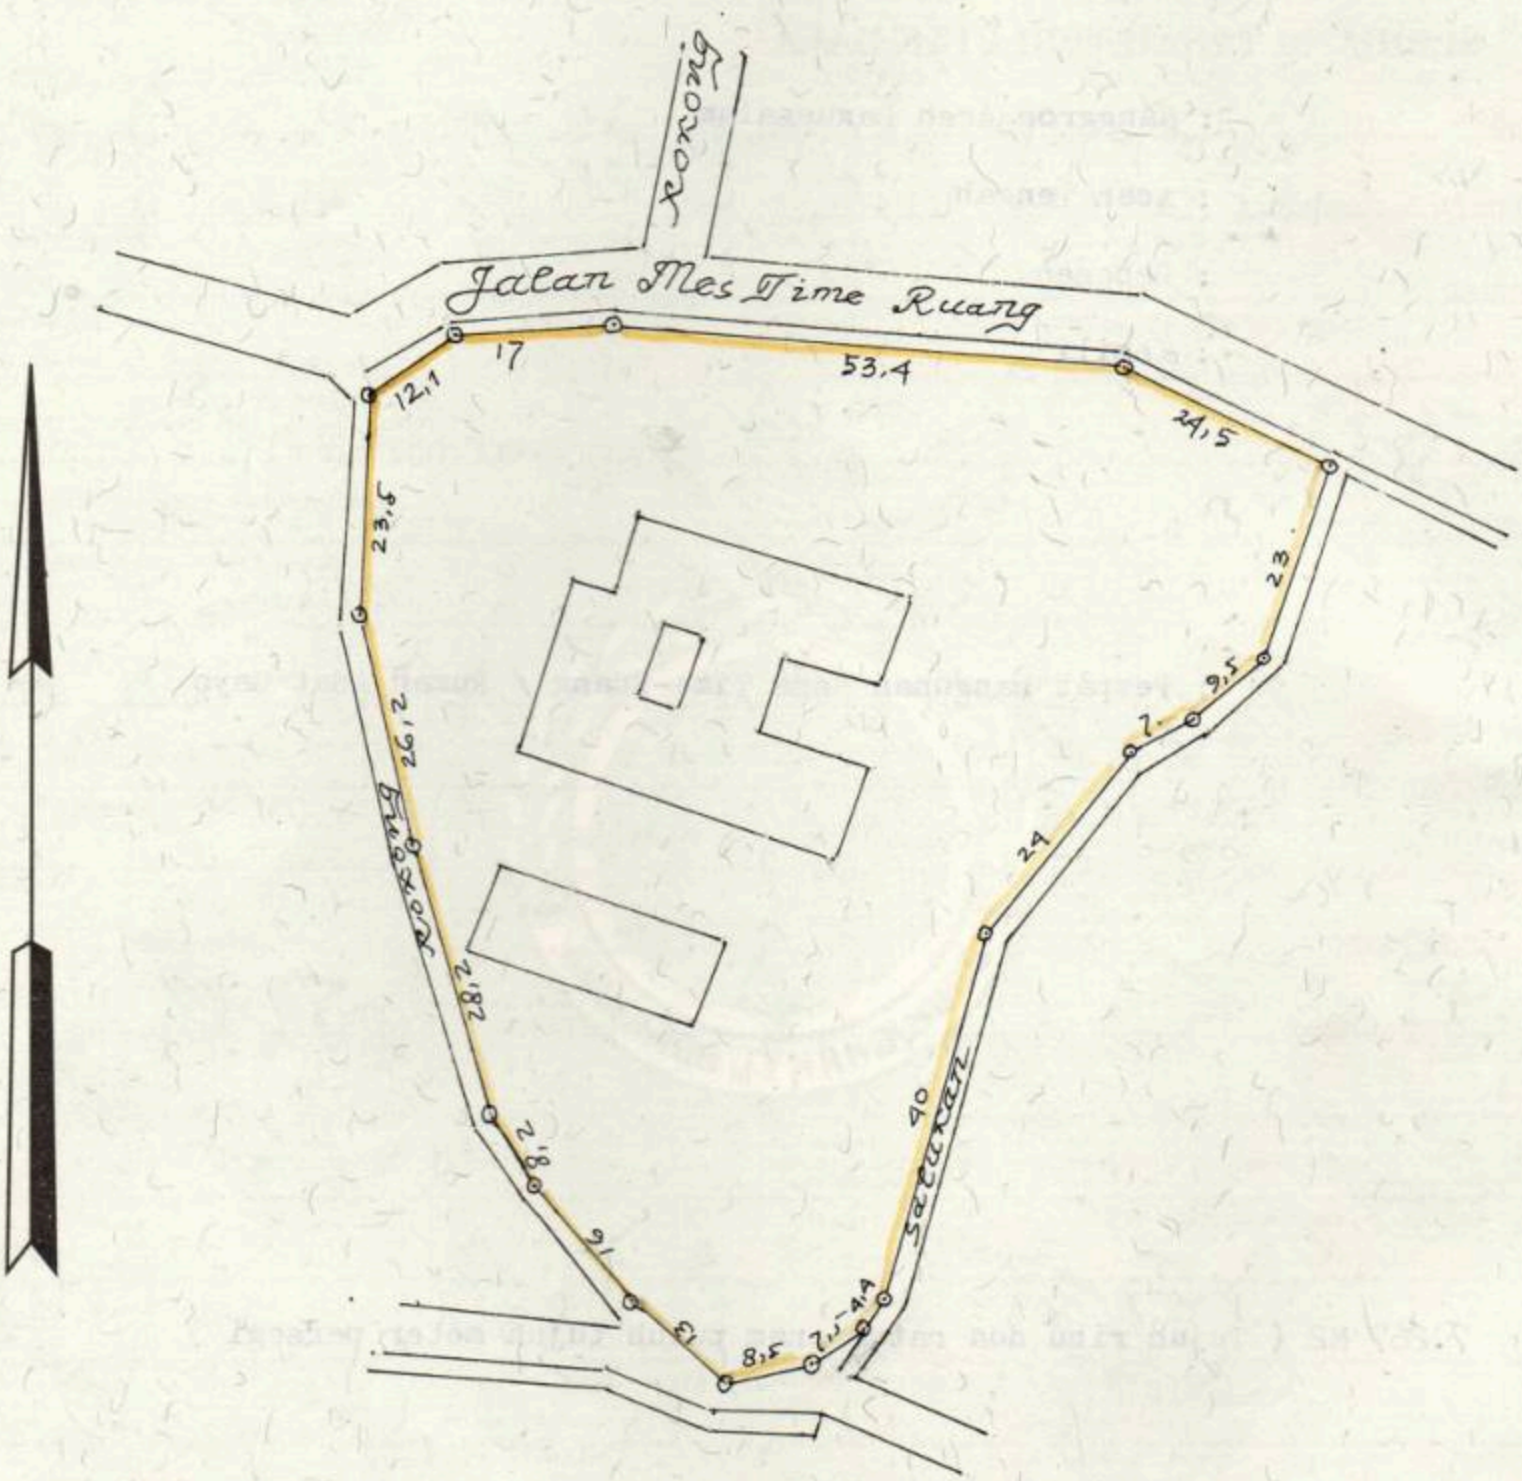

PENJELASAN : _____ **batas tanah ini**

Hal lain - lain : .....

.....

.....

.....

Daftar Isian 302 tgl. 28-9-2004 No. 299

Daftar Isian 307 tgl. ..... No. .....

UNTUK SERTIPIKAT

Takengon , Tgl. 28 - 05 - 2005

Kepala Kantor Pertanahan
Kabupaten / ~~Kotamadya~~
Aceh Tengah

=. DRS. BUDI YAZIR .=

NIP 010172837

Takengon , Tgl. 28 - 05 - 2005

Kepala Seksi Pengukuran dan Pendaftaran Tanah

Kantor Pertanahan
Kabupaten / ~~Kotamadya~~
Aceh Tengah

ttd.

=. M. TAUFIK, S.Si .=

NIP 010196016

Lihat surat ukur Pemisahan / Penggabungan / Pengganti Nomor ..... / 200.. Nomor hak : .....

Dikeluarkan surat ukur		Luas	Nomor hak	Sisa luas
Tanggal	Nomor			

Sisanya diuraikan dalam surat ukur Nomor : ..... / 200..... Nomor hak .....