BUDI LUHUR

BA 277595

DAFTAR ISIAN 206

BADAN PERTANAHAN NASIONAL REPUBLIK INDONESIA

10

SERTIPIKAT

(TANDA BUKTI HAK)

KANTOR PERTANAHAN
KABUPATEN / KOTA

.....

0	1	•	0	9	•	0	2	•	0	7	•	2	•	0	0	0	0	8			

BA 277595

DAFTAR ISIAN 206

BADAN PERTANAHAN NASIONAL REPUBLIK INDONESIA

SERTIPIKAT

HAK : PAKAI **No.** 8

PROPINSI : NANGGROE ACEH DARUSSALAM

KABUPATEN / KOTA : ACEH TENGAH

KECAMATAN : BEBESEN

D E S A/ KELURAHAN : KEMILI

DAFTAR ISIAN 307
No. .....
DAFTAR ISIAN 208
No. 3103 /2009

KANTOR PERTANAHAN KABUPATEN / KOTA

ACEH TENGAH

01 • 09 • 02 • 07 • 2 • 00008

PENDAFTARAN - PERTAMA

Halaman :

a) HAK : PAKAI
No. : 8
Desa / Kel. : Kemili
Tgl. berakhirnya hak :

b) NIB 01.09.02.07.00495
Letak Tanah

f) NAMA PEMEGANG HAK

PEMERINTAH KABUPATEN ACEH TENGAH

Tanggal lahir / akta pendirian

c) ASAL HAK

1. Konversi
2. Pemberian hak
3. Pemecahan / Pemisahan / Penggabungan bidang — P. 2 dan 7

d) DASAR PENDAFTARAN

1. Daftar Isian 202
   Tgl.
   No.
2. Surat Keputusan
   Tgl.
   No.
3. Permohonan Pemecahan / Pemisahan / Penggabungan bidang
   Tgl.
   No.

e) SURAT UKUR

Tgl. 31 Juli 2009
No. 79 /2009
Luas. 7.929.5 M2

g) PEMBUKUAN

Takengon Tgl. 03 Agustus 2009
Kepala Kantor Pertanahan
Kabupaten / Kota
Aceh Tengah

ttd

DRS. HAMDAN

NIP 19541107 197803 1 002

h) PENERBITAN SERTIPIKAT

Takengon Tgl. 03 Agustus 2009

Kepala Kantor Pertanahan
Kabupaten / Kota
Aceh Tengah

BADAN PERTANAHAN NASIONAL REPUBLIK INDONESIA

DRS. HAMDAN

NIP 19541107 197803 1 002

i) PENUNJUK

Berdasarkan Surat Permohonan Penggabungan Sertipikat Hak Pakai No. 2 dan 7 Tanggal 27 Juli 2009

DAFTAR ISIAN 207

01 • 09 • 02 • 07 • 2 • 00008

NIB : 01.09.02.07.00495

SURAT UKUR

Nomor : 79 / 2009

SEBIDANG TANAH TERLETAK DALAM

Propinsi : Nanggroe Aceh Darussalam

Kabupaten / Kota : Aceh Tengah

Kecamatan : Bebesen

Desa /Kelurahan : Kemili

Peta : Nomor Peta Pendaftaran :

Lembar : Kotak :


Keadaan Tanah : Sebidang tanah Pertanian

Tanda-tanda batas :

Luas : 7.929.5 M2 (Tujuh ribu sembilan ratus dua puluh sembilan koma lima meter persegi)

Penunjukan dan penetapan batas : *Drs. H. Djauhar Ali*

SKALA 1 : 1000

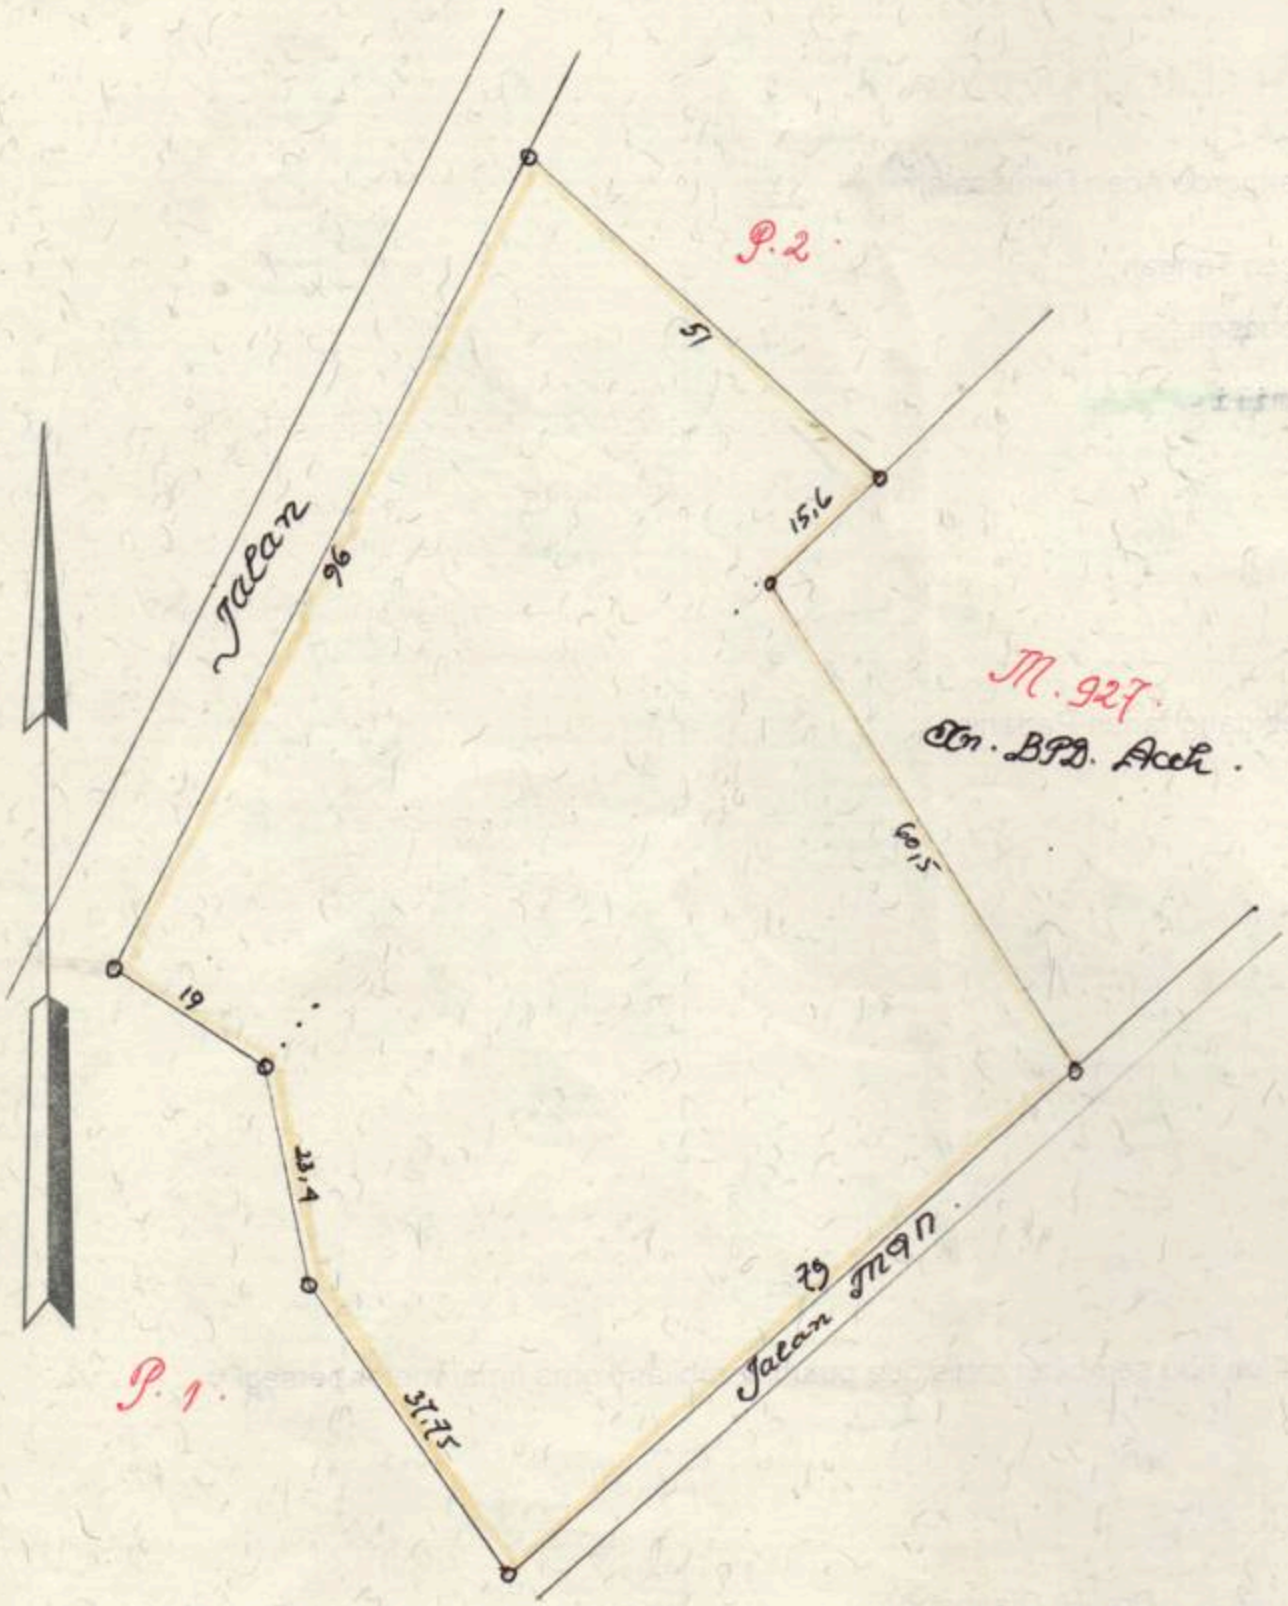

PENJELASAN : _____ batas tanah ini

Hal lain - lain :

Daftar Isian 302 tgl. 31 Juli 2009 No. 839

Daftar Isian 307 tgl. No.

Tanggal Penomoran Surat Ukur

UNTUK SERTIPIKAT

Takengon Tgl. 31 Juli 2009

Kepala Seksi Survei, Pengukuran dan Pemetaan

Kantor Pertanahan
Kabupaten / Kota
Aceh Tengah

ttd

ERWIS, Aptnh

NIP 19650607 198603 1 003

Takengon Tgl. 03 Agustus 2009

Kepala Kantor Pertanahan
Kabupaten / Kota
Aceh Tengah

DRS. HAMDAN

NIP 19541107 197803 1 002

Lihat surat ukur Pemisahan / Penggabungan / Pengganti

Nomor : Nomor hak :

Dikeluarkan surat ukur		Luas	Nomor hak	Sisa luas
Tanggal	Nomor			

Sisanya diuraikan dalam surat ukur Nomor : Nomor hak :