BADAN PERTANAHAN NASIONAL

BUKU TANAH

HAK : PAKAI. No. 7

PROPINSI : DAERAH ISTIMEWA ACEH.

KABUPATEN/~~KOTAMADYA~~ : ACEH TENGAH.

KECAMATAN : KOTA TAKENGON.

DESA/~~KELURAHAN~~ : BALE ATU.

KANTOR PERTANAHAN
KABUPATEN/~~KOTAMADYA~~
ACEH TENGAH

DAFTAR ISIAN 208
No. 15. /19 98.

DAFTAR ISIAN 307
No. 61. /19 98.

01 · 09 · 01 · 13 · 4 · 00007

PENDAFTARAN - PERTAMA

Halaman :

a) HAK : PAKAI.

No. : 7

Desa : Bale Atu.

b) NAMA JALAN/PERSIL

Jalan Pasar Inpres.

c) ASAL PERSIL

1. ~~Konversi~~

2. Pemberian hak pakai.

3. ~~Pemisahan~~

4. ~~Penggabungan~~

d) SURAT KEPUTUSAN

KEPALA KANTOR WILAYAH BADAN-PERTANAHAN NASIONAL PROPINSI DAERAH ISTIMEWA ACEH.
NOMOR : 48/HPJ/BPN/1997-1998
TANGGAL , 31 DESEMBER 1997.

Uang pemasukan/biaya administrasi
Rp.15.000,- PNBP.No.11/II/98
Tanggal , 14-2-1998.

Lamanya hak berlaku selama diper gunakan untuk keperluan dinas

Berakhirnya hak

Tgl.

e) ~~SURAT UKUR~~ / GAMBAR SITUASI

Tgl. 19-2-1998.

No. 13.

Luas 5.100 M2.

f) NAMA PEMEGANG HAK

=.PEMERINTAH KABUPATEN DAERAH TK.II ACEH TENGAH
yang berkedudukan di TAKENGON.=

g) PEMBUKUAN

Takengon , Tgl. 19-2-1998.

Kepala Kantor Pertanahan
Kabupaten/~~Kotamadya~~
Aceh Tengah

ttd.

=. ERIONO SONO .=

NIP 010038411

h) PENERBITAN SERTIPIKAT

Takengon , Tgl. 19-2-1998

Kepala Kantor Pertanahan
Kabupaten/~~Kotamadya~~
Aceh Tengah

BADAN PERTANAHAN NASIONAL 01 REPUBLIK INDONESIA 03

=. ERIONO SONO .=

NIP 010038411

i) PENUNJUK

01	09	01	13	4	00007

DAFTAR ISIAN 207

Nomor hak : 7

SURAT UKUR

GAMBAR SITUASI

Nomor : 13 /1998 : -

SEBIDANG TANAH TERLETAK DALAM

Propinsi : : Daerah Istimewa Aceh.

Kabupaten/~~Kotamadya~~ : : Aceh Tengah.

Kecamatan : : Kota Takengon.

Desa/~~Kelurahan~~ : : Bale Atu.

Peta : .....

Lembar : ..... Kotak : ..... Nomor Pendaftaran : .....


Keadaan Tanah : : Sebidang tanah diatasnya terdapat bangunan Kios Inpres.

Tanda-tanda batas : .....

Luas : 5.100 M2. (Lima ribu seratus meter persegi)

Penunjukan dan penetapan batas : oleh Pemohon dan Kepala Desa.

PERBANDINGAN 1 : 1000.-

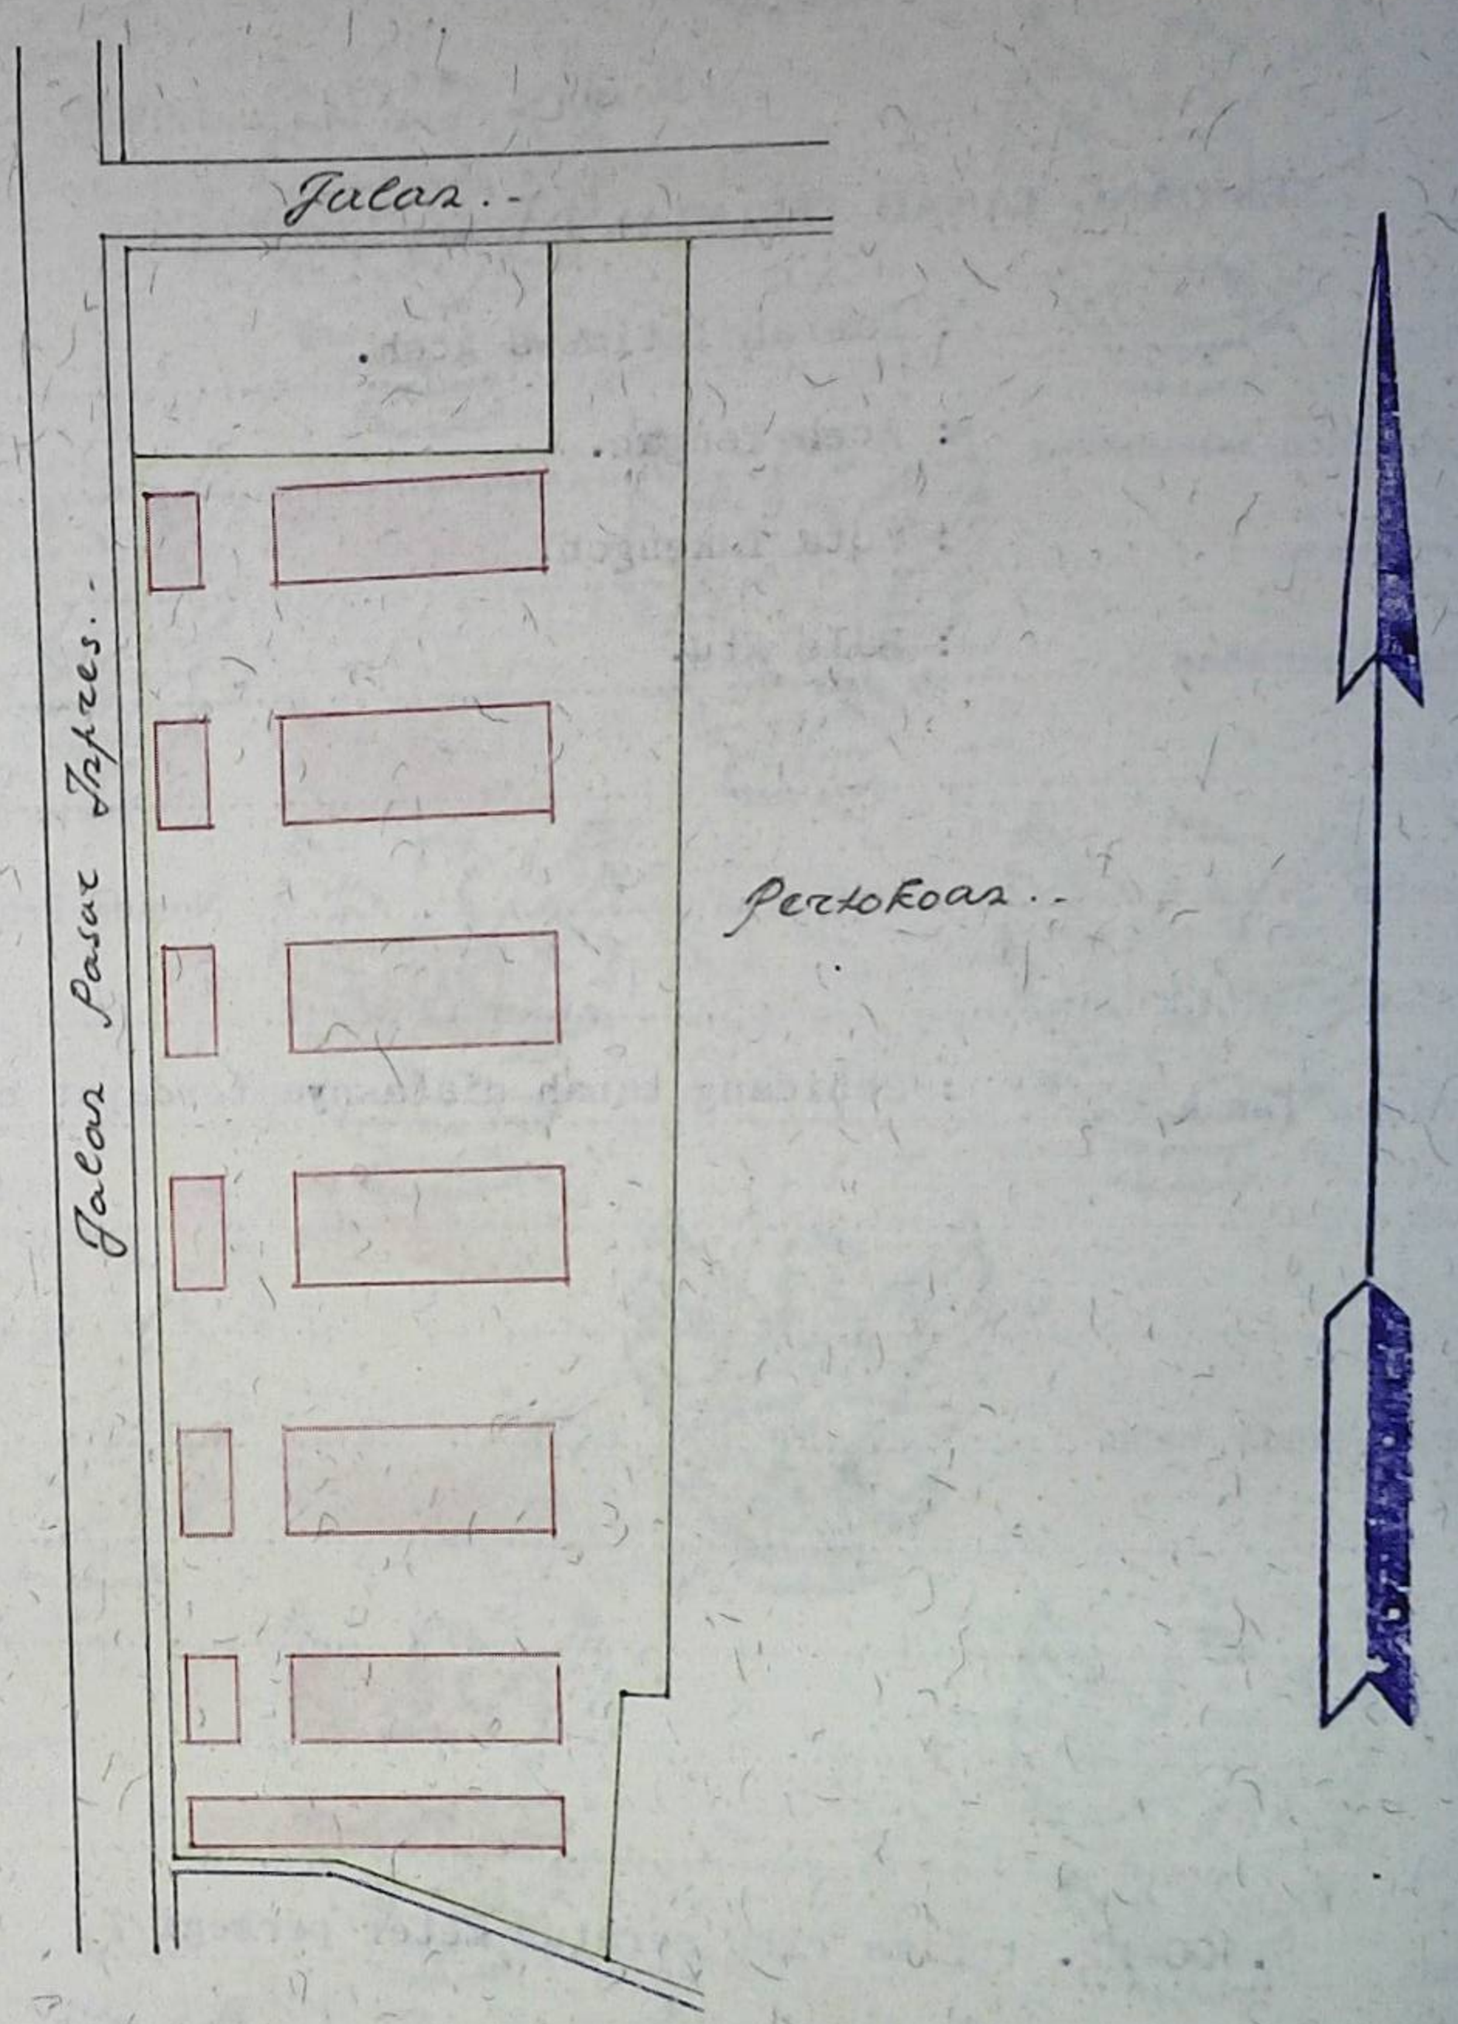

PENJELASAN : ..... batas tanah ini

Hal lain-lain : Gambar Situasi ini adalah merupakan Petikan dari Peta Situasi No.01.09/ 33/PPL/1997, Tgl. 10-5-1997.

Daftar Isian 303 tgl. 19-2-1998. No. 47.

Daftar Isian 307 tgl. 19-2-1998. No. 62.

UNTUK SERTIPIKAT

Takengon , Tgl. 19-2-1998 19...

Kepala Kantor Pertanahan
Kabupaten/~~Kotamadya~~
Aceh Tengah

=. ERIONO SONO .=

NIP 010038411

Takengon , Tgl. 19-2-1998 19...

Kepala Seksi Pengukuran dan Pendaftaran Tanah
Kantor Pertanahan
Kabupaten/~~Kotamadya~~
Aceh Tengah

ttd

=. ZAINAL ABBAS.SH .=

NIP 010083877

Lihat surat ukur / gambar situasi Pemisahan / Penggabungan / Pengganti Nomor : ...../19..... Nomor hak : .....

Dikeluarkan surat ukur/gambar situasi		Luas	Nomor hak	Sisa luas
Tanggal	Nomor			

Sisanya diuraikan dalam surat ukur / gambar situasi Nomor : ...../19..... Nomor hak .....