Kab. Aceh Tengah Pemda Tk II Terminal Bebesen Kecamatan

DAFTAR ISIAN 206

BADAN PERTANAHAN NASIONAL

7

SERTIPIKAT

(TANDA BUKTI HAK)

KANTOR PERTANAHAN

KABUPATEN/~~KOTAMADYA~~

ACEH TENGAH

Kec.	**: Kec. Bebesen**
No. Urut	**: 7**
Alamat	: Kemili
No. Sertifikat	: 01.09.02.07.4.00005
Tahun	: 19 Februari 1998
Peruntukan	: Tanah Terminal (Bangunan Terminal)
SKPK	**: Dinas Perhubungan**

AG 703678

01 · 09 · 02 · 07 · 4 · 00005

BADAN PERTANAHAN NASIONAL



BUKU TANAH

HAK : PAKAI. No. ~~17~~ 5

PROPINSI : DAERAH ISTIMEWA ACEH.

KABUPATEN/~~KOTAMADYA~~ : ACEH TENGAH.

KECAMATAN : BEBESEN.

D E S A/~~KELURAHAN~~ : KEMILI.

KANTOR PERTANAHAN
KABUPATEN/~~KOTAMADYA~~

ACEH TENGAH

DAFTAR ISIAN 208
No. 17. /19 98.

DAFTAR ISIAN 307
No. 65. /19 98.

0	1	·	0	9	·	0	2	·	0	7	·	4	·	0	0	0	0	5

PENDAFTARAN - PERTAMA

Halaman :

a) HAK : PAKAI.

No. : ~~1 7~~ 5

Desa : Kemili.

b) NAMA JALAN/PERSIL

Jalan Terminal/Sengeda.

c) ASAL PERSIL

1. ~~Konversi~~
2. Pemberian hak pakai.
3. ~~Pemisahan~~
4. ~~Penggabungan~~

d) SURAT KEPUTUSAN

KEPALA KANTOR WILAYAH BADAN-PERTANAHAN NASIONAL PROPINSI DAERAH ISTIMEWA ACEH.
NOMOR : 48/HPJ/BPN/1997-1998
TANGGAL , 31 DESEMBER 1997.

Uang pemasukan/biaya administrasi
Rp.15.000,- PNBP.No.10/II/98
Tanggal , 14-2-1998.

Lamanya hak berlaku selama diper gunakan untuk keperluan dinas.

Berakhirnya hak

Tgl.

e) ~~SURAT UKUR~~
GAMBAR SITUASI

Tgl. 19-2-1998.

No. 15.

Luas 5.902 M2.

f) NAMA PEMEGANG HAK

=.PEMERINTAH KABUPATEN DAERAH TK.II ACEH TENGAH yang berkedudukan di TAKENGON.=

g) PEMBUKUAN

Takengon , Tgl. 19-2-1998.

Kepala Kantor Pertanahan
Kabupaten/~~Kotamadya~~
Aceh Tengah

ttd.

=. ERIONO SONO .=

NIP 010038411

h) PENERBITAN SERTIPIKAT

Takengon , Tgl. 19-2-1998.

Kepala Kantor Pertanahan
Kabupaten/~~Kotamadya~~
Aceh Tengah

BADAN PERTANAHAN NASIONAL REPUBLIK INDONESIA

=. ERIONO SONO .=

NIP 010038411

i) PENUNJUK

DAFTAR ISIAN 207

01	09	02	07	4	00005

Nomor hak : ~~174~~ 5

~~SURAT UKUR~~
GAMBAR SITUASI

Nomor : 15. /1998.

SEBIDANG TANAH TERLETAK DALAM

Propinsi : : Daerah Istimewa Aceh.

Kabupaten/~~Kotamadya~~ : : Aceh Tengah.

Kecamatan : : Bebesen.

Desa/~~Kelurahan~~ : : Kemili.

Peta :

Lembar : Kotak : Nomor Pendaftaran :


Keadaan Tanah : : Sebidang tanah diatasnya terdapat bangunan permanen (terminal)

Tanda-tanda batas :

Luas : 5.902 M2. (Lima ribu sembilan ratus dua meter persegi)

Penunjukan dan penetapan batas : oleh Pemohon dan Kepala Desa.

PERBANDINGAN 1 : 1.000.-

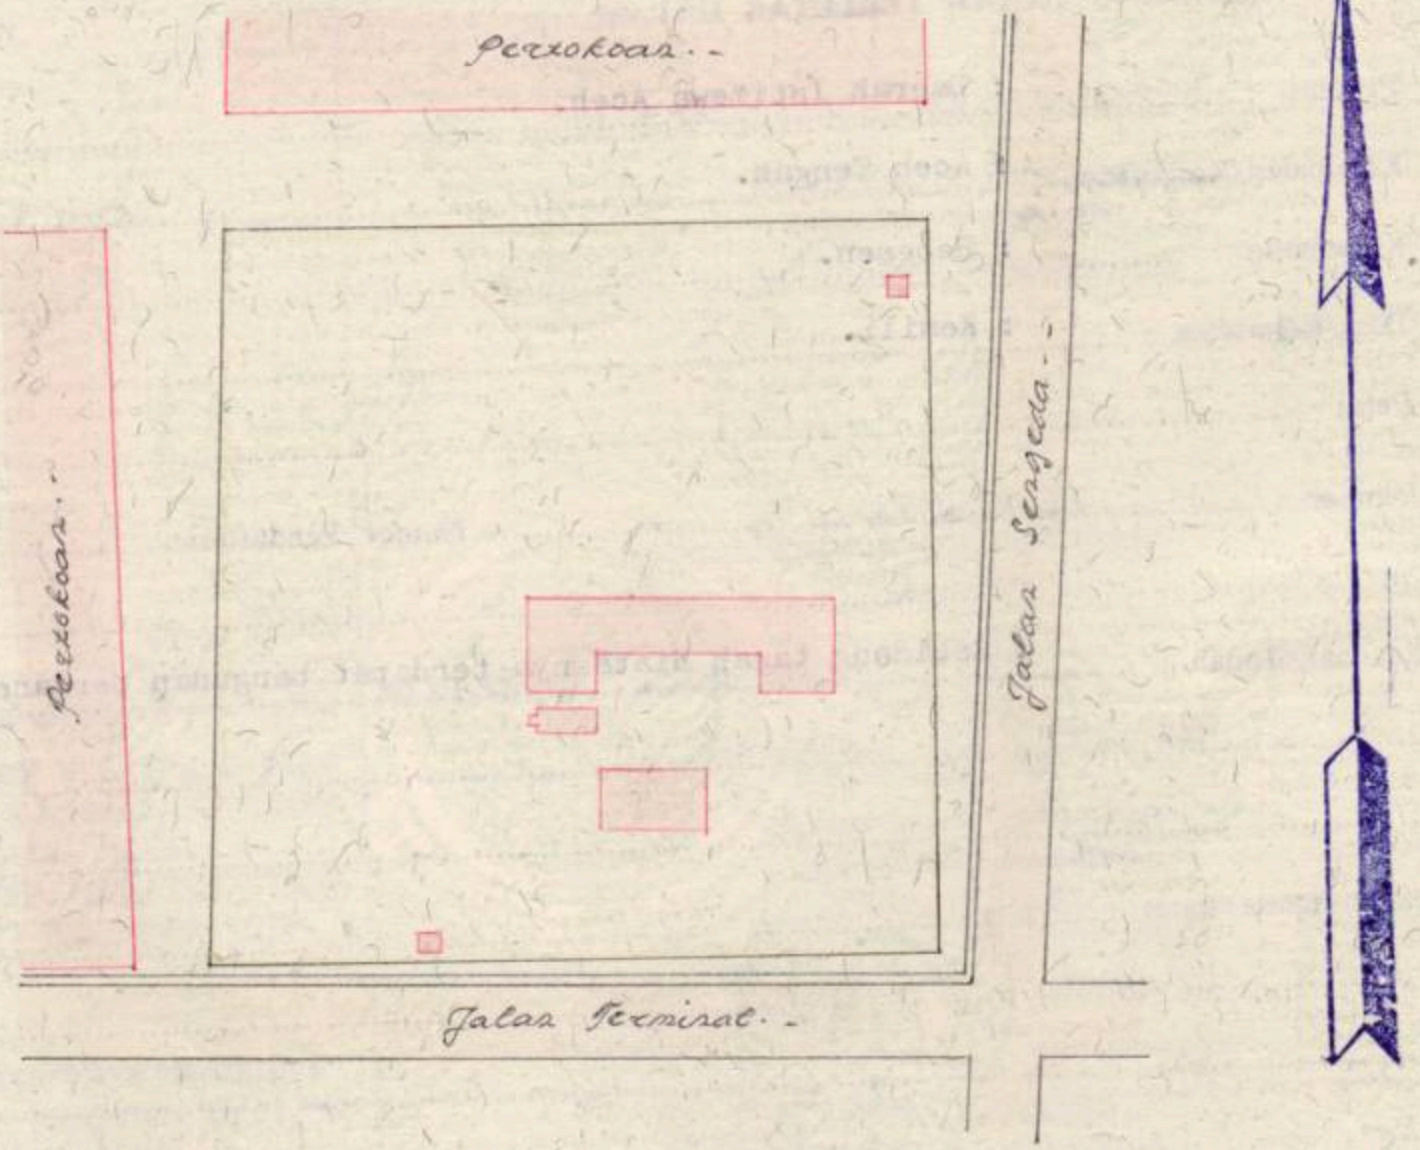

PENJELASAN : ..... batas tanah ini

Hal lain-lain : Gambar Situasi ini adalah merupakan Petikan dari Peta Situasi No.01.09/35/PPL/1997, Tgl. 10-5-1997.

Daftar Isian 302 tgl. 19-2-1998. No. 49.

Daftar Isian 307 tgl. 19-2-1998. No. 66.

UNTUK SERTIPIKAT

Takengon , Tgl. 19-2-1998 19...

Kepala Kantor Pertanahan
Kabupaten/~~Kotamadya~~
Aceh Tengah

=. ERIONO SONO .=

NIP 010038411

Takengon , Tgl. 19-2-1998 19...

Kepala Seksi Pengukuran dan Pendaftaran Tanah

Kantor Pertanahan
Kabupaten/~~Kotamadya~~
Aceh Tengah

ttd

=. ZAINAL ABBAS.SH .=

NIP 010083877

Lihat surat ukur / gambar situasi Pemisahan / Penggabungan / Pengganti Nomor : ...../19..... Nomor hak : .....

Dikeluarkan surat ukur/gambar situasi		Luas	Nomor hak	Sisa luas
Tanggal	Nomor			

Sisanya diuraikan dalam surat ukur / gambar situasi Nomor : ...../19..... Nomor hak .....