AY 639030

DAFTAR ISIAN 206

BADAN PERTANAHAN NASIONAL



SERTIPIKAT

HAK : PAKAI No. 44

PROPINSI : NANGGROE ACEH DARUSSALAM

KABUPATEN / ~~KOTAMADYA~~ : ACEH TENGAH

KECAMATAN : LUT TAWAR

DESA / ~~KELURAHAN~~ : TAKENGON BARAT

KANTOR PERTANAHAN
KABUPATEN / ~~KOTAMADYA~~
ACEH TENGAH

DAFTAR ISIAN 307
No. ..... / 200.....
DAFTAR ISIAN 208
No. 546 / 200.5..

01 • 09 • 01 • 10 • 4 • 00044

PENDAFTARAN - PERTAMA

Halaman :

a) HAK : : PAKAI
No. : : 44
Desa / Kel. : Takengon Barat
Tgl. berakhirnya hak :
Selama di Pakai

b) NIB 01.09.01.10.00028
Letak Tanah

c) ASAL HAK
1. ~~Konversi~~
2. Pemberian hak Pakai
3. ~~Pemecahan / Pemisahan / Penggabungan bidang~~

d) DASAR PENDAFTARAN
1. Daftar Isian 202
Tgl.
No.
2. Surat Keputusan
Tgl. 30-04-2005
No. 8/HP/BPN/2005
3. Permohonan Pemecahan / Pemisahan / Penggabungan bidang
Tgl.
No.

e) SURAT UKUR
Tgl. 28-05-2005
No. 01. / 2005
Luas. 8.412 M2

f) NAMA PEMEGANG HAK
=.PEMERINTAH KABUPATEN ACEH TENGAH-
berkedudukan di- TAKENGON.=

Tanggal lahir / akta pendirian

g) PEMBUKUAN
Takengon , Tgl. 13 Mei 2005
Kepala Kantor Pertanahan
Kabupaten / ~~Kotamadya~~
Aceh Tengah
ttd.
=. DRS.BUDI YAZIR .=
NIP 010172837

h) PENERBITAN SERTIPIKAT
Takengon , Tgl. 28 Mei 2005
Kepala Kantor Pertanahan
Kabupaten / ~~Kotamadya~~
Aceh Tengah
=. DRS.BUDI YAZIR .=
NIP 010172837

i) PENUNJUK

0	1	•	0	9	•	0	1	•	1	0	•	4	•	0	0	0	4	4

DAFTAR ISIAN 207

NIB : 01.09.01.10.00028

SURAT UKUR

Nomor : ..... 01 ..... / 2005...

SEBIDANG TANAH TERLETAK DALAM

Propinsi : ..... : Nanggroe Aceh Darussalam .....

Kabupaten / ~~Kotamadya~~ : ..... : Aceh Tengah .....

Kecamatan : ..... : Lut Tawar .....

Desa / ~~Kelurahan~~ : ..... : Takengon Barat .....

Peta : ..... Nomor Peta Pendaftaran : .....

Lembar : ..... Kotak : .....

.....

Keadaan Tanah : ..... : Sebidang tanah diatasnya terdapat bangunan Gedung SMP.Negeri I .....

.....

.....

.....

Tanda-tanda batas : .....

.....

.....

.....

.....

Luas : 8.412 M2 (Delapan ribu empat ratus dua belas meter persegi) .....

.....


.....

Penunjukan dan penetapan batas : oleh Pemohon dan Kepala Desa .....

.....

.....

SKALA 1 : 1000

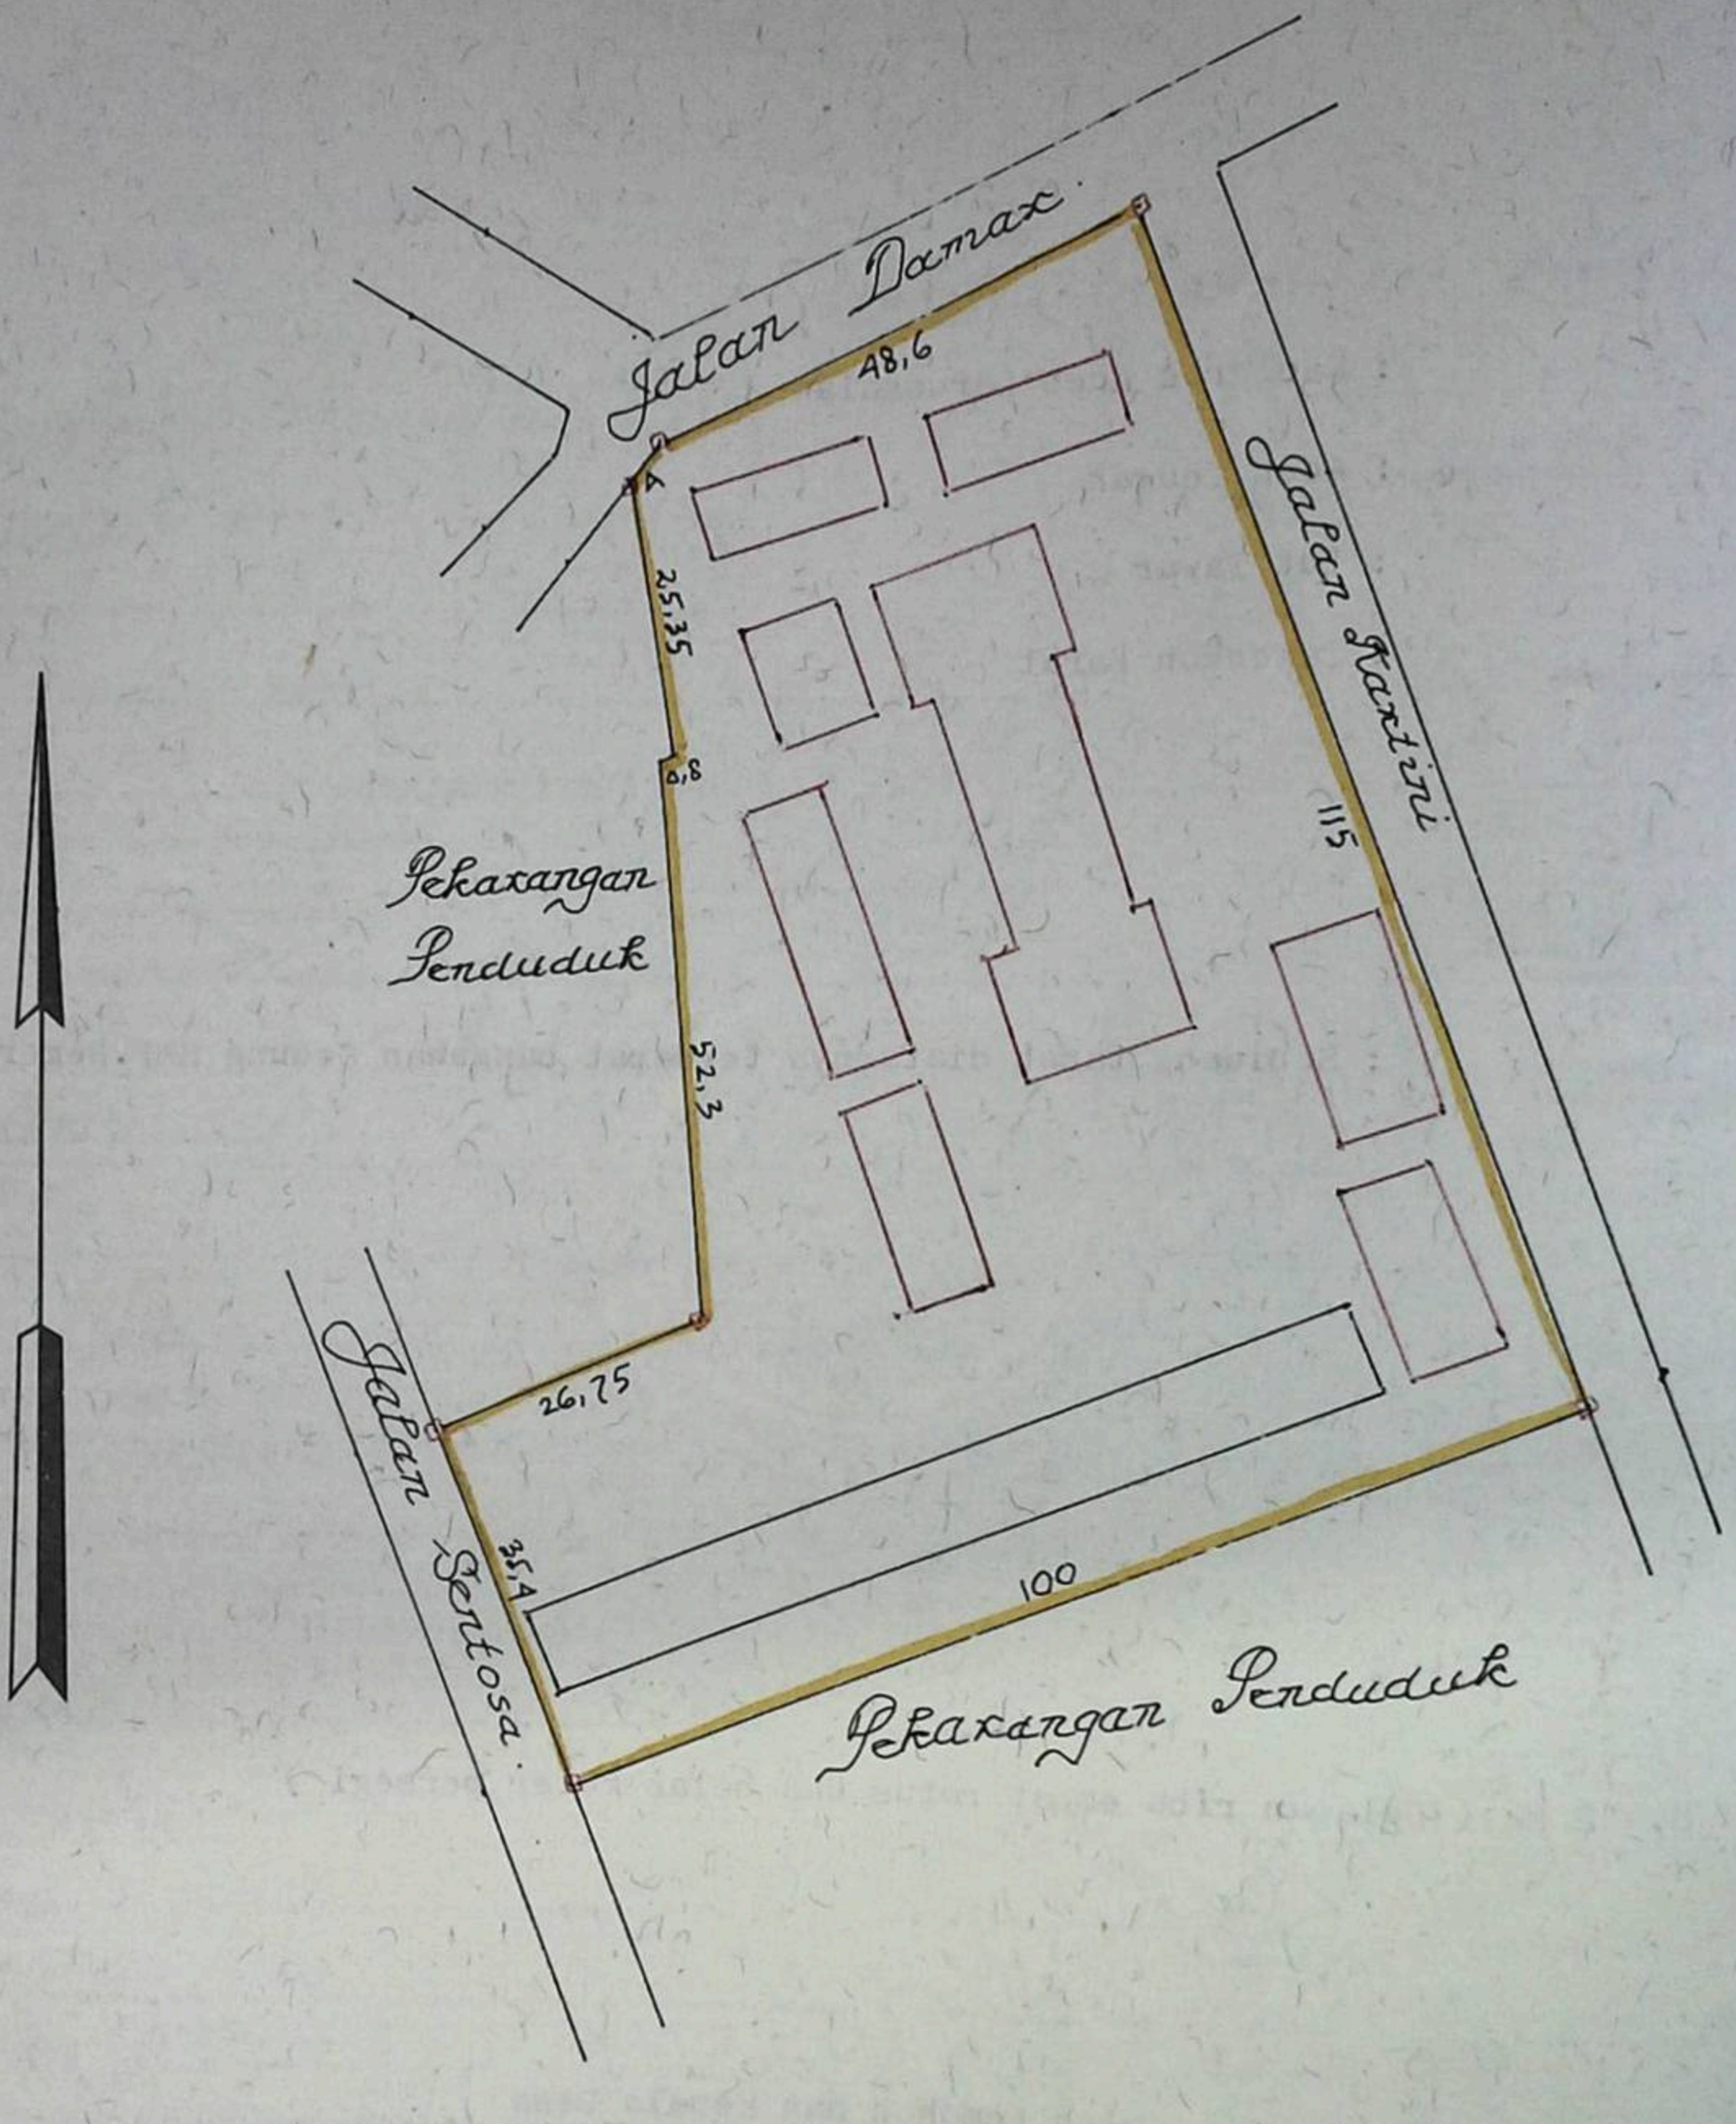

PENJELASAN : _____ **batas tanah ini**

Hal lain - lain : .....

.....

.....

.....

Daftar Isian 302 tgl. 28 - 9 - 2004 No. 299

Daftar Isian 307 tgl. ..... No. .....

UNTUK SERTIPIKAT

Takengon , Tgl. 28 Mei 200.5

Kepala Kantor Pertanahan
Kabupaten / ~~Kotamadya~~
Aceh Tengah

ttd.

Drs. BUDI YAZIR

NIP 010172837

Takengon , Tgl. 28 Mei 200.5

Kepala Seksi Pengukuran dan Pendaftaran Tanah

Kantor Pertanahan
Kabupaten / ~~Kotamadya~~
Aceh Tengah

ttd.

M. TAUFIK, S.Si

NIP 010190016

Lihat surat ukur Pemisahan / Penggabungan / Pengganti Nomor : ..... / 200.. Nomor hak : .....

Dikeluarkan surat ukur		Luas	Nomor hak	Sisa luas
Tanggal	Nomor			

Sisanya diuraikan dalam surat ukur Nomor : ..... / 200..... Nomor hak .....