AAC554584

DAFTAR ISIAN 206

KEMENTERIAN AGRARIA DAN TATA RUANG / BADAN PERTANAHAN NASIONAL REPUBLIK INDONESIA

SERTIPIKAT

(TANDA BUKTI HAK)

NO. 40
Tanah kurang parkir kendaraan
dinas Lingkungan hidup
Kp. Sodong
Kec. Baboshan luas 8.464 m²

KANTOR PERTANAHAN
KABUPATEN / KOTA

.....

0	1	•	0	9	•	0	2	•	2	8	•	2	•	0	0	0	0	1			

AAC554584

DAFTAR ISIAN 206

KEMENTERIAN AGRARIA DAN TATA RUANG / BADAN PERTANAHAN NASIONAL REPUBLIK INDONESIA

SERTIPIKAT

PAKAI *01*

HAK : ..... **No.** .....

PROVINSI : *ACEH*

KABUPATEN / KOTA : *ACEH TENGAH*

KECAMATAN : *BEBESEN*

D E S A / KELURAHAN : *SADONG JURU MUDI*

DAFTAR ISIAN 307
No. .....
DAFTAR ISIAN 208
No. ...../2017

KANTOR PERTANAHAN
KABUPATEN / KOTA

ACEH TENGAH

01 • 09 • 02 • 28 • 2 • 00001

PENDAFTARAN - PERTAMA

Halaman :

a) HAK : PAKAI 01

No. : Sadong Juru Mudi

Desa / Kel. :

Tgl. berakhirnya hak :

b) NIB 01.09.02.28.00018

Letak Tanah

f) NAMA PEMEGANG HAK

PEMERINTAH KABUPATEN ACEH TENGAH

Berkedudukan di Takengon.

Tanggal lahir / akta pendirian

c) ASAL HAK

1. Konversi

Pakai

2. Pemberian Hak

3. Pemecahan / Pemisahan / Penggabungan bidang

g) PEMBUKUAN

Takengon Tgl. 10 April 2018

.....

Kepala Kantor Pertanahan

Kabupaten / Kota Aceh Tengah

.....

ttd

ERWIS, A.Ptnh

.....

NIP. 19650607 198603 1003

d) DASAR PENDAFTARAN

1. Daftar Isian 202

Tgl.

No.

2. Surat Keputusan

Tgl. 05 April 2018

No. 09/HP/BPN.01-09/IV /2018

3. Permohonan Pemecahan / Pemisahan / Penggabungan bidang

Tgl.

No.

h) PENERBITAN SERTIPIKAT

Takengon Tgl. 10 April 2018

.....

Kepala Kantor Pertanahan

Kabupaten / Kota Aceh Tengah

.....

ERWIS, A.Ptnh

.....

NIP. 19650607 198603 1003

e) SURAT UKUR 13 November 2017

Tgl. 14 /2017

No. 8,464 M2

Luas :

i) PENUNJUK

AAC554584

01	•	09	•	02	•	28	•	2	•	0	0	0	0	1

DAFTAR ISIAN 207

NIB : 01.09.02.28.00018

SURAT UKUR

Nomor : 14 /2017

SEBIDANG TANAH TERLETAK DALAM

Provinsi : Aceh

Kabupaten / Kota : Aceh Tengah

Kecamatan : Bebesen

Desa /Kelurahan : Sedong Juru Mudi

Peta : Nomor Peta Pendaftaran :

Lembar : Kotak :


Keadaan Tanah : Sebidang tanah digunakan untuk Gudang dan Tempat Parkir Kendaraan Dinas Operasional Kantor Lingkungan Hidup Kabupaten Aceh Tengah

Tanda-tanda batas :

Luas : 8,464 M2 (Delapan ribu empat ratus enam puluh empat meter persegi)

Penunjukan dan penetapan batas : Ir. Zikriadi, MM

SKALA 1 : 1.000,-

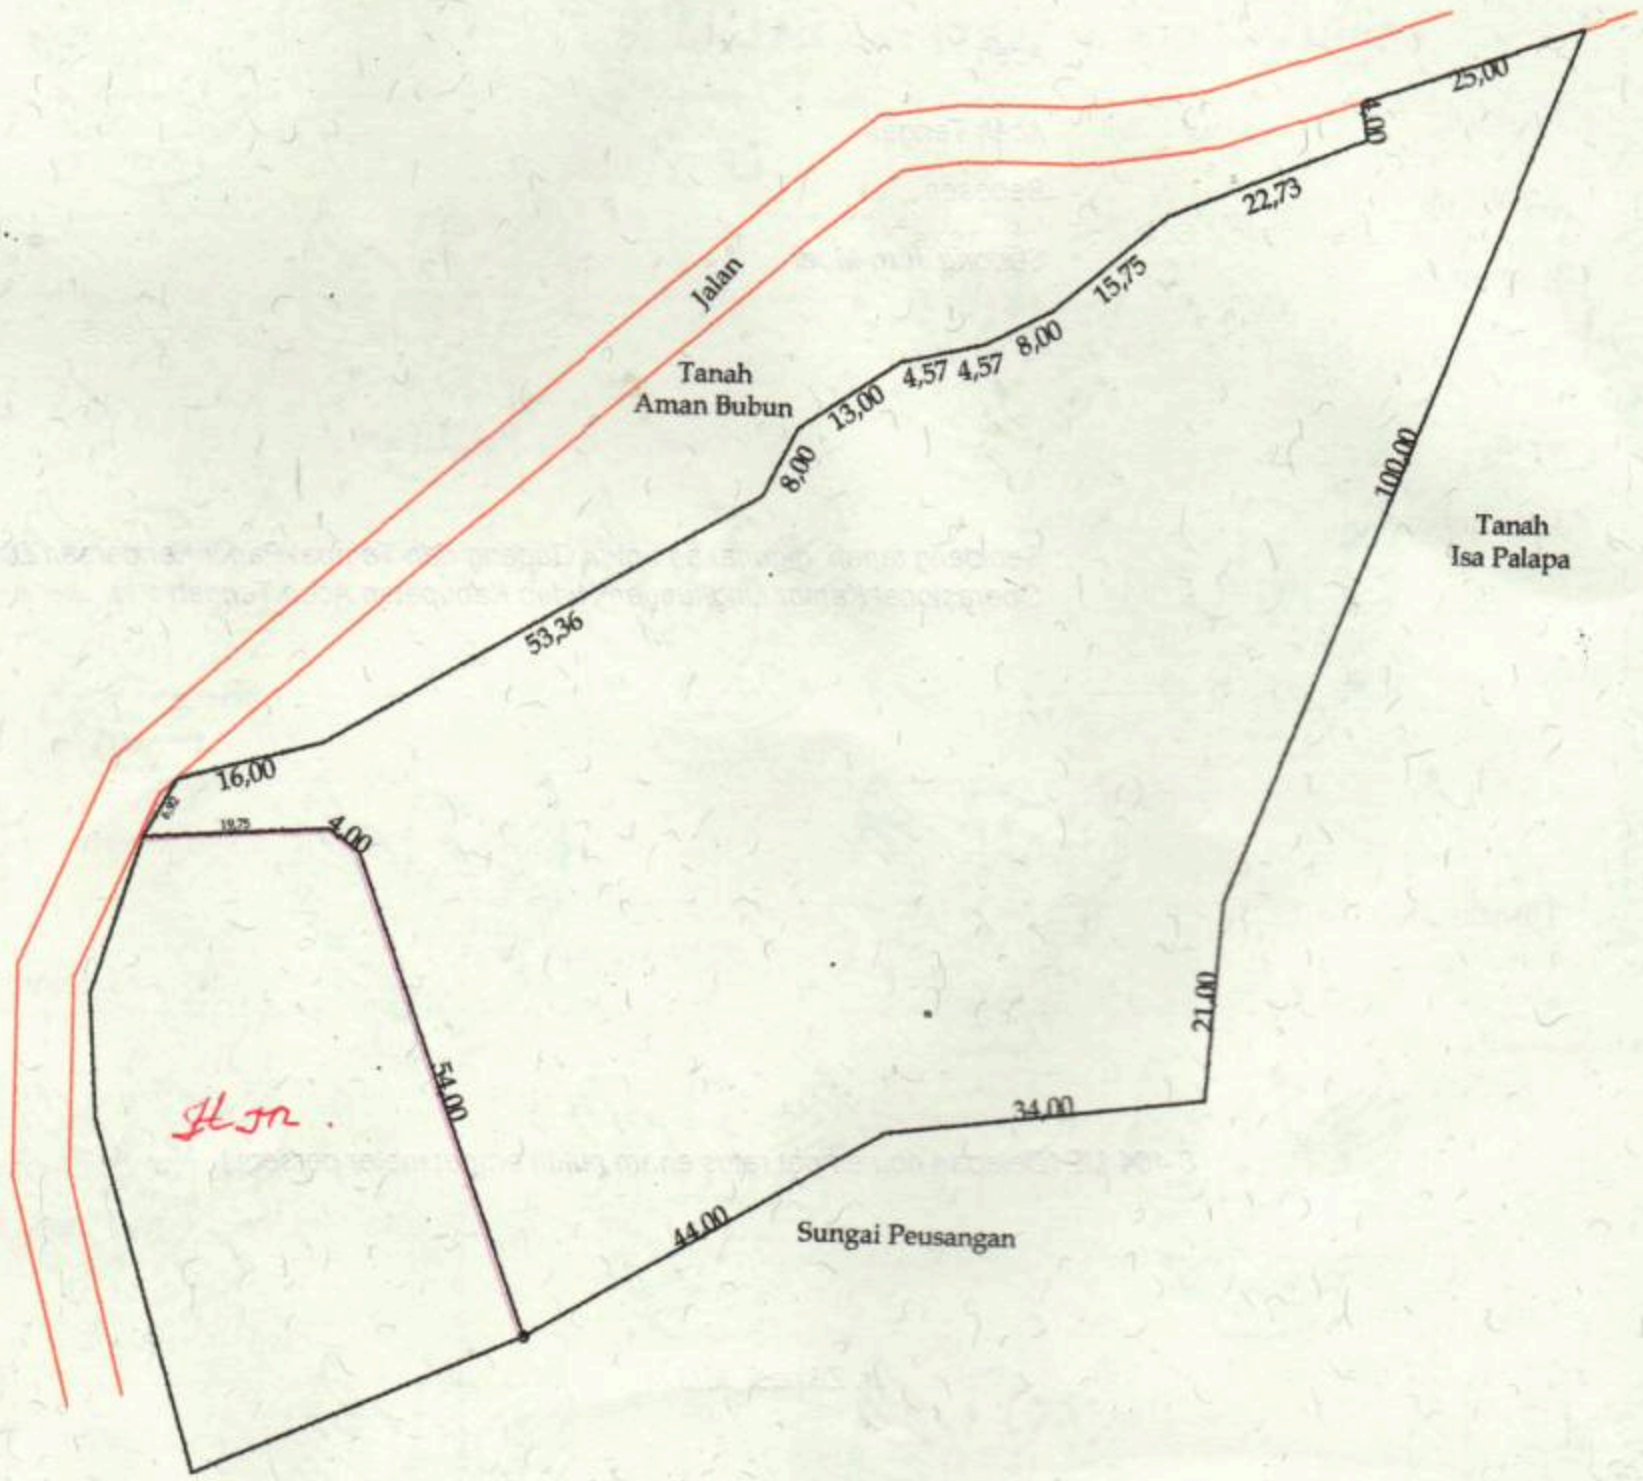

PRODUCED BY AN AUTODESK EDUCATIONAL PRODUCT

PENJELASAN : ..... **batas tanah ini**

Hal lain - lain :

Daftar Isian 302 tgl. 13 November 2017 No. 3193

Daftar Isian 307 tgl. No.

Tanggal Penomoran Surat Ukur

Takengon Tgl. 13 November 2017

UNTUK SERTIPIKAT

Takengon Tgl. Tgl. 10 April 2018

Kepala Seksi Infrastruktur Pertanahan

Kepala Kantor Pertanahan
Kabupaten / Kota

Kantor Pertanahan
Kabupaten / Kota

ttd

ERWIS, A.Ptnh

EDI PRANATA,S.ST

NIP 19680607 198803 1 003

NIP 197807151999031005

Lihat surat ukur Pemisahan / Penggabungan / Pengganti

Nomor : Nomor hak :

Dikeluarkan surat ukur		Luas	Nomor hak	Sisa luas
Tanggal	Nomor			

Sisanya diuraikan dalam surat ukur Nomor : ..... Nomor hak .....