BH 730971

DAFTAR ISIAN 206

BADAN PERTANAHAN NASIONAL
REPUBLIK INDONESIA

SERTIPIKAT
(TANDA BUKTI HAK)

Kec. : Kec. Bebesen
No. Urut : 31
Alamat : Empus Talu
No. Sertifikat : 01.09.02.23.1.00003
Tahun : 28 Maret 2014
Peruntukan : Puskesmas Empus Talu
SKPK : Dinas Kesehatan

KANTOR PERTANAHAN
KABUPATEN / KOTA

.....

6	1	•	0	9	•	0	2	•	2	3	•	1	•	0	0	0	0	3

BH 730971

DAFTAR ISIAN 206

BADAN PERTANAHAN NASIONAL REPUBLIK INDONESIA

SERTIPIKAT

PAKAI *03*

HAK : ..... **No.** .....

PROVINSI : *ACEH*

KABUPATEN / KOTA : *ACEH TENGAH*

KECAMATAN : *BEBESEN*

D E S A/ KELURAHAN : *EMPUS TALU*

DAFTAR ISIAN 307
No. .....
DAFTAR ISIAN 208 *552* */2014*
No. .....

KANTOR PERTANAHAN
KABUPATEN / KOTA
ACEH TENGAH

0	1	•	0	9	•	0	2	•	2	3	•	1	•	0	0	0	0	3

Halaman :

PENDAFTARAN - PERTAMA

a) HAK : PAKAI
No. : 03
Desa / Kel. : Empus Talu
Tgl. berakhirnya hak :

b) NIB 01.09.02.23.00118
Letak Tanah

f) NAMA PEMEGANG HAK

PEMERINTAH KABUPATEN ACEH TENGAH

Tanggal lahir / akta pendirian

c) ASAL HAK

1. Konversi
2. Pemberian hak Pakai
3. Pemecahan / Pemisahan / Penggabungan bidang

g) PEMBUKUAN

Takengon Tgl. 28 Maret 2014

Kepala Kantor Pertanahan
Kabupaten / Kota
Aceh Tengah

ttd.

DRS. FAUZI

NIP 196712311994031011

d) DASAR PENDAFTARAN

1. Daftar Isian 202
   Tgl.
   No.
2. Surat Keputusan
   Tgl. 10 Pebruari 2014
   No. 04/HP/BPN.01-09/II/2014
3. Permohonan Pemecahan / Pemisahan / Penggabungan bidang
   Tgl.
   No.

h) PENERBITAN SERTIPIKAT

Takengon Tgl. 28 Maret 2014

Kepala Kantor Pertanahan
Kabupaten / Kota
Aceh Tengah

DRS. FAUZI

NIP 196712311994031011

e) SURAT UKUR

Tgl. 10 Januari 2014
No. 34 /2014
Luas. 1,149 M2

i) PENUNJUK

BH 730971

0	1	•	0	9	•	0	2	•	2	3	•	1	•	0	0	0	0	3

DAFTAR ISIAN 207

NIB : 01.09.02.23.00118

SURAT UKUR

Nomor : 34 /2014

SEBIDANG TANAH TERLETAK DALAM

Provinsi : Aceh

Kabupaten / Kota : Aceh Tengah

Kecamatan : Bebesen

Desa /Kelurahan : Empus Talu

Peta : 47.1 Nomor Peta Pendaftaran : 16.289-07-9

Lembar : Kotak :


Keadaan Tanah : Sebidang tanah pekarangan

Tanda-tanda batas : Berupa patok besi yang dipasang pada setiap sudut batas

Luas : 1,149 M2 (Seribu seratus empat puluh sembilan meter persegi)

Penunjukan dan penetapan batas : Pemohon dan Kepala Kampung

SKALA 1 : 500

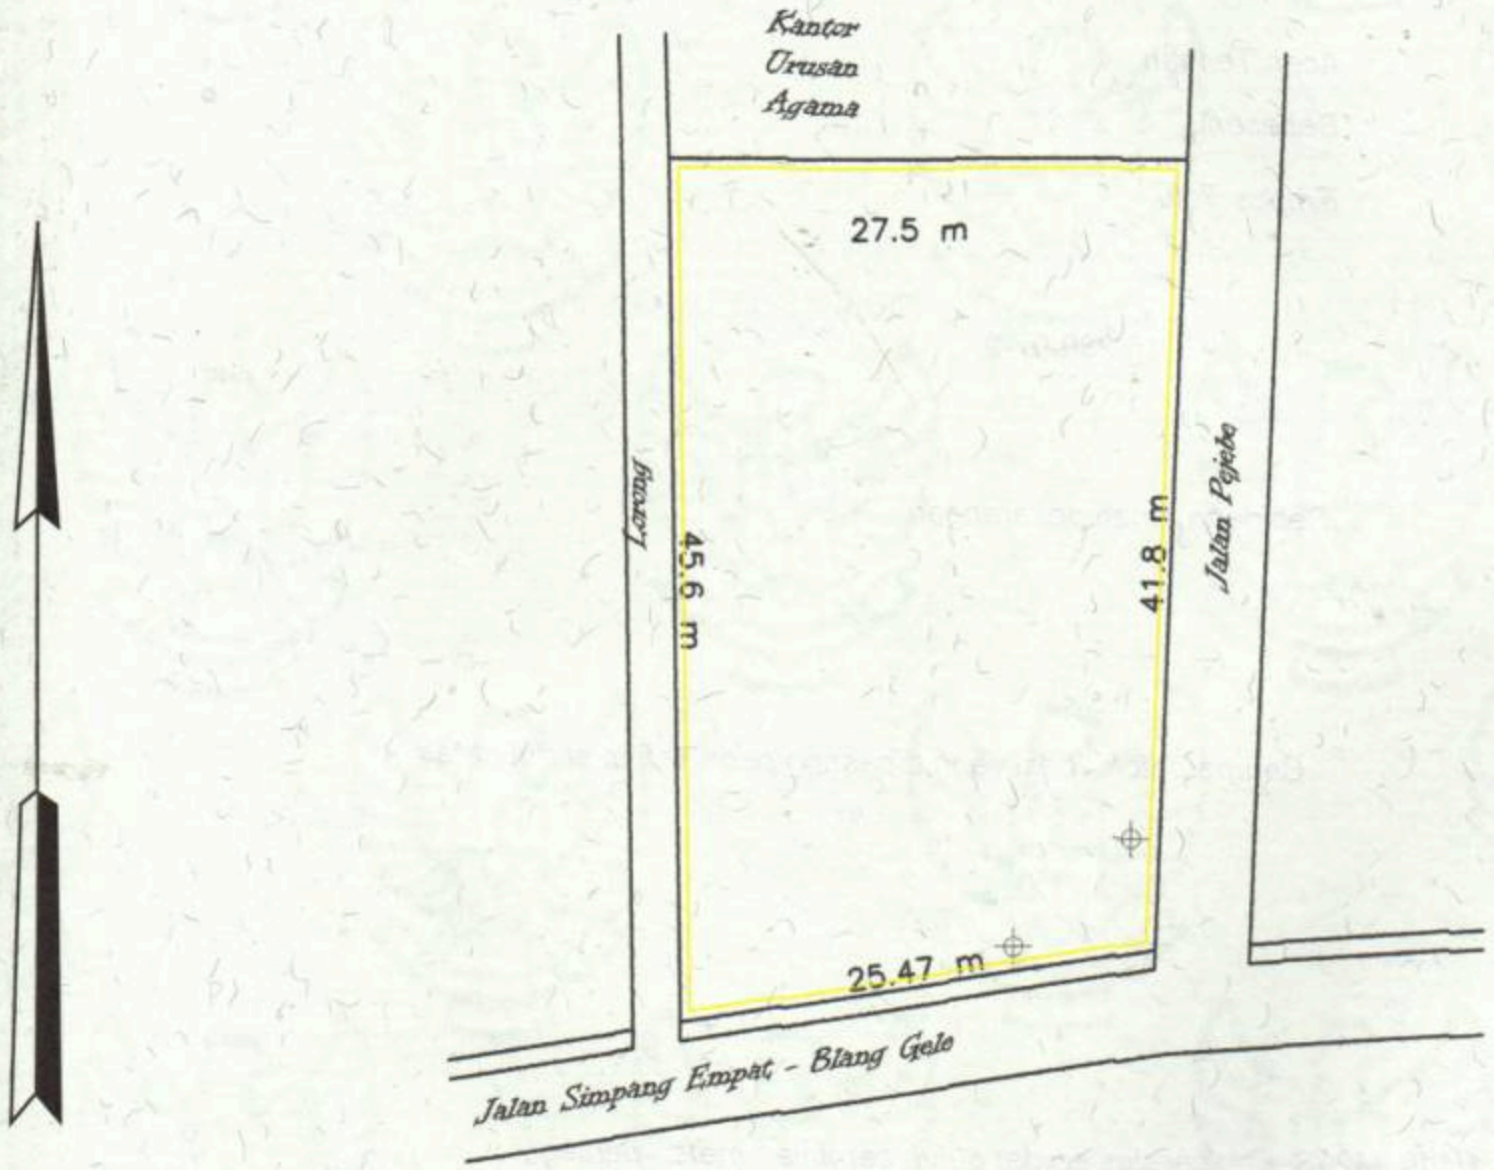

PENJELASAN : ..... **batas tanah ini**

Hal lain - lain :

Daftar Isian 302 tgl. 12 Desember 2013 No. 2157

Daftar Isian 307 tgl. 28 Maret 2014 No. 1104

Tanggal Penomoran Surat Ukur

UNTUK SERTIPIKAT

Takengon Tgl. 10 Januari 2014

Takengon Tgl. Tgl. 28 Maret 2014

Kepala Seksi Survei, Pengukuran dan Pemetaan

Kepala Kantor Pertanahan
Kabupaten / Kota
Aceh Tengah

Kantor Pertanahan
Kabupaten / Kota
Aceh Tengah

ttd

Drs. FAUZI

NIP 196712311994031011

EDI PRANATA, S.ST

NIP 197807151999031005

Lihat surat ukur Pemisahan / Penggabungan / Pengganti

Nomor : Nomor hak :

Dikeluarkan surat ukur		Luas	Nomor hak	Sisa luas
Tanggal	Nomor			

Sisanya diuraikan dalam surat ukur Nomor : Nomor hak :