AT 593707

Puskesmas Pegasing

DAFTAR ISIAN 206

BADAN PERTANAHAN NASIONAL





SERTIPIKAT

(TANDA BUKTI HAK)

KANTOR PERTANAHAN
KABUPATEN / KOTAMADYA

ACEH TENGAH

Kec. : Kec. Pegasing
No. Urut : 1
Alamat : Simpang Kelaping
No. Sertifikat : 01.09.09.05.4.00004
Tahun : 27 Februari 2003
Peruntukan : Tanah Puskesmas Pegasing
SKPK : Dinas Kesehatan

01 • 09 • 09 • 05 • 4 • 00004

Scanned with CamScanner

T 593707

DAFTAR ISIAN 206

BADAN PERTANAHAN NASIONAL

SERTIPIKAT

HAK : PAKAI No. 04

PROPINSI : NANGGROE ACEH DARUSSALAM

KABUPATEN / KOTAMADYA : ACEH TENGAH

KECAMATAN : PEGASING

DESA/ KELURAHAN : SIMPANG KELAPING

DAFTAR ISIAN 307
No. ..... / 200.....
DAFTAR ISIAN 208
No. .....67... / 200..3..

KANTOR PERTANAHAN
KABUPATEN / KOTAMADYA

ACEH TENGAH

01 • 09 • 09 • 05 • 4 • 00004

Scanned with CamScanner

a) HAK : PAKAI
No. 04
Desa / Kel. : Simpang Kelaping
Tgl. berakhirnya hak :

b) NIB 01.09.09.05.00031
Letak Tanah

c) ASAL HAK
1. Konversi
2. Pemberian hak Pakai
3. Pemecahan / Pemisahan / Penggabungan bidang

d) DASAR PENDAFTARAN
1. Daftar Isian 202
Tgl.
No.
2. Surat Keputusan
Tgl. 18 Pebruari 2003
No. 5/HP/BPN/2003
3. Permohonan Pemecahan / Pemisahan / Penggabungan bidang
Tgl.
No.

e) SURAT UKUR
Tgl. 11 Januari 2003
No. 01
Luas 2.204 M2

f) NAMA PEMEGANG HAK
PEMERINTAH KABUPATEN ACEH TENGAH

Tanggal lahir / akta pendirian

g) PEMBUKUAN
Takengon, Tgl. 27 Pebruari 2003
Kepala Kantor Pertanahan
Kabupaten / Kotamadya
Aceh Tengah

ttd.

= DRS. BUDI YAZIR =
NIP 010172837

h) PENERBITAN SERTIPIKAT
Takengon, Tgl. 27 Pebruari 2003
Kepala Kantor Pertanahan
Kabupaten / Kotamadya
Aceh Tengah

a.n.

= DRS. BUDI YAZIR =
NIP 010 172 837

i) PENUNJUK

BHUMIBHAKTI RENUGUNA
BADAN PERTANAHAN NASIONAL REPUBLIK INDONESIA
Scanned with CamScanner

DAFTAR ISIAN 207

01 • 09 • 09 • 05 • 4 • 00004

NIB : 01.09.09.05.00031

SURAT UKUR

Nomor : .....01...../ 200..3..

SEBIDANG TANAH TERLETAK DALAM

Propinsi : Nanggroe Aceh Darussallam

Kabupaten / Kotamadya : Aceh Tengah

Kecamatan : Pegasing

Desa / Kelurahan : Simpang Kelaping

Peta : ..... Nomor Peta Pendaftaran : .....

Lembar : ..... Kotak : .....

Keadaan Tanah : Sebidang tanah untuk Bangunan Puskesmas Pegasing


Tanda-tanda batas : Berupa patok beton yang dipasang pada tiap-tiap sudut batas

Luas : 2.204 M^2 (Dua ribu dua ratus empat meter persegi)

Penunjukan dan penetapan batas : Dr. Malida

Scanned with CamScanner

SKALA 1 : 500

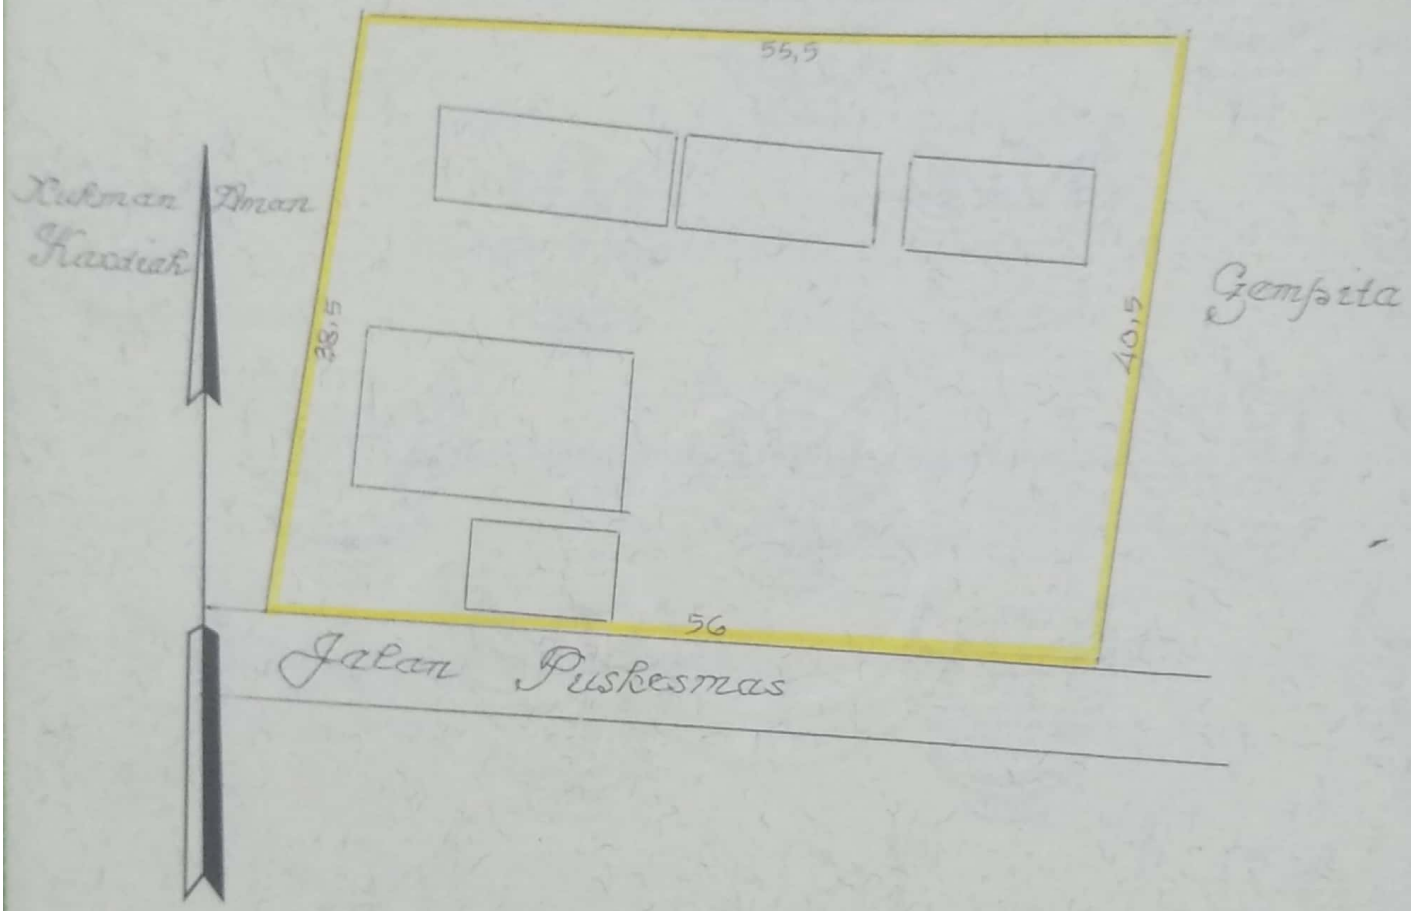

PENJELASAN : _____ batas tanah ini

Scanned with CamScanner

Hal lain - lain

Daftar Isian 302 tgl. 8 Januari 2003 No. 8

Daftar Isian 307 tgl. ..... No. .....

UNTUK SERTIPIKAT

Takengon Tgl. *27 Pebruari* 200.. *3*

Kepala Kantor Pertanahan
Kabupaten / Kotamadya
Aceh Tengah

DRS. HUDI YAZIR

NIP 010 172 837

Takengon Tgl. *11 Januari* 200.. *2*

Kepala Seksi Pengukuran dan Pendaftaran Tanah

Kantor Pertanahan
Kabupaten / Kotamadya
Aceh Tengah

ttd.

ZAHARI, SH

NIP 010 104 801

Lihat surat ukur Pemisahan / Penggabungan / Penggantí Nomor ..... / 200.. Nomor hak : .....

Dikeluarkan surat ukur		Luas	Nomor hak	Sisa luas
Tanggal	Nomor			

Sisanya diuraikan dalam surat ukur Nomor ..... / 200..... Nomor hak .....

Scanned with CamScanner