AT 593707

Puskesmas Pegasing

DAFTAR ISIAN 206

BADAN PERTANAHAN NASIONAL





SERTIPIKAT

(TANDA BUKTI HAK)

KANTOR PERTANAHAN
KABUPATEN / KOTAMADYA

ACEH TENGAH

Kec. : Kec. Pegasing
No. Urut : 1
Alamat : Simpang Kelaping
No. Sertifikat : 01.09.09.05.4.00004
Tahun : 27 Februari 2003
Peruntukan : Tanah Puskesmas Pegasing
SKPK : Dinas Kesehatan

01 • 09 • 09 • 05 • 4 • 00004

Scanned with CamScanner

T 593707

DAFTAR ISIAN 206

BADAN PERTANAHAN NASIONAL



SERTIPIKAT

HAK : PAKAI No. 04

PROPINSI : NANGGROE ACEH DARUSSALAM

KABUPATEN / KOTAMADYA : ACEH TENGAH

KECAMATAN : PEGASING

DESA/ KELURAHAN : SIMPANG KELAPING

DAFTAR ISIAN 307
No. ..... / 200.....
DAFTAR ISIAN 208
No. .....67... / 200..3..

KANTOR PERTANAHAN
KABUPATEN / KOTAMADYA

ACEH TENGAH

0	1	•	0	9	•	0	9	•	0	5	•	A	•	0	0	0	0	4			

Scanned with CamScanner

a) HAK : PAKAI

No. 04

Desa / Kel. : Simpang Kelaping

Tgl. berakhirnya hak :

b) NIB 01.09.09.05.00031

Letak Tanah

c) ASAL HAK

1. Konversi

2. Pemberian hak Pakai

3. Pemecahan / Pemisahan / Penggabungan bidang

d) DASAR PENDAFTARAN

1. Daftar Isian 202

Tgl.

No.

2. Surat Keputusan

Tgl. 18 Pebruari 2003

No. 5/HP/BPN/2003

3. Permohonan Pemecahan / Pemisahan / Penggabungan bidang

Tgl.

No.

e) SURAT UKUR

Tgl. 11 Januari 2003

No. 01

Luas 2.204 M2

f) NAMA PEMEGANG HAK

PEMERINTAH KABUPATEN ACEH TENGAH

Tanggal lahir / akta pendirian

g) PEMBUKUAN

Takengon, Tgl. *27 Pebruari 2003*

Kepala Kantor Pertanahan
Kabupaten / Kotamadya
Aceh Tengah

ttd

= DRS. BUDI YAZIR =

NIP 010172837

h) PENERBITAN SERTIPIKAT

Takengon Tgl. *27 Pebruari 2003*

Kepala Kantor Pertanahan
Kabupaten / Kotamadya
Aceh Tengah

= DRS. BUDI YAZIR =

NIP 010 172 837

i) PENUNJUK

Scanned with CamScanner

DAFTAR ISIAN 207

0	1	•	0	9	•	0	9	•	0	5	•	4	•	0	0	0	0	4

NIB : 01.09.09.05.00031

SURAT UKUR

Nomor : ..... 01 ..... / 200 3 ..

SEBIDANG TANAH TERLETAK DALAM

Propinsi : ..... Nanggroe Aceh Darussallam .....

Kabupaten / Kotamadya : ..... Aceh Tengah .....

Kecamatan : ..... Pegasing .....

Desa / Kelurahan : ..... Simpang Kelaping .....

Peta : ..... Nomor Peta Pendaftaran : .....

Lembar : ..... Kotak : .....

.....

Keadaan Tanah : ..... Sebidang tanah untuk Bangunan Puskesmas Pegasing .....

.....

Tanda-tanda batas : ..... Berupa patok beton yang dipasang pada tiap-tiap sudut batas .....

.....

.....

.....

.....

Luas : ..... 2.204 M^2 (Dua ribu dua ratus empat meter persegi) .....

.....

.....

Penunjukan dan penetapan batas : ..... Dr. Malida .....


.....

.....

.....

Scanned with CamScanner

SKALA 1 : 500

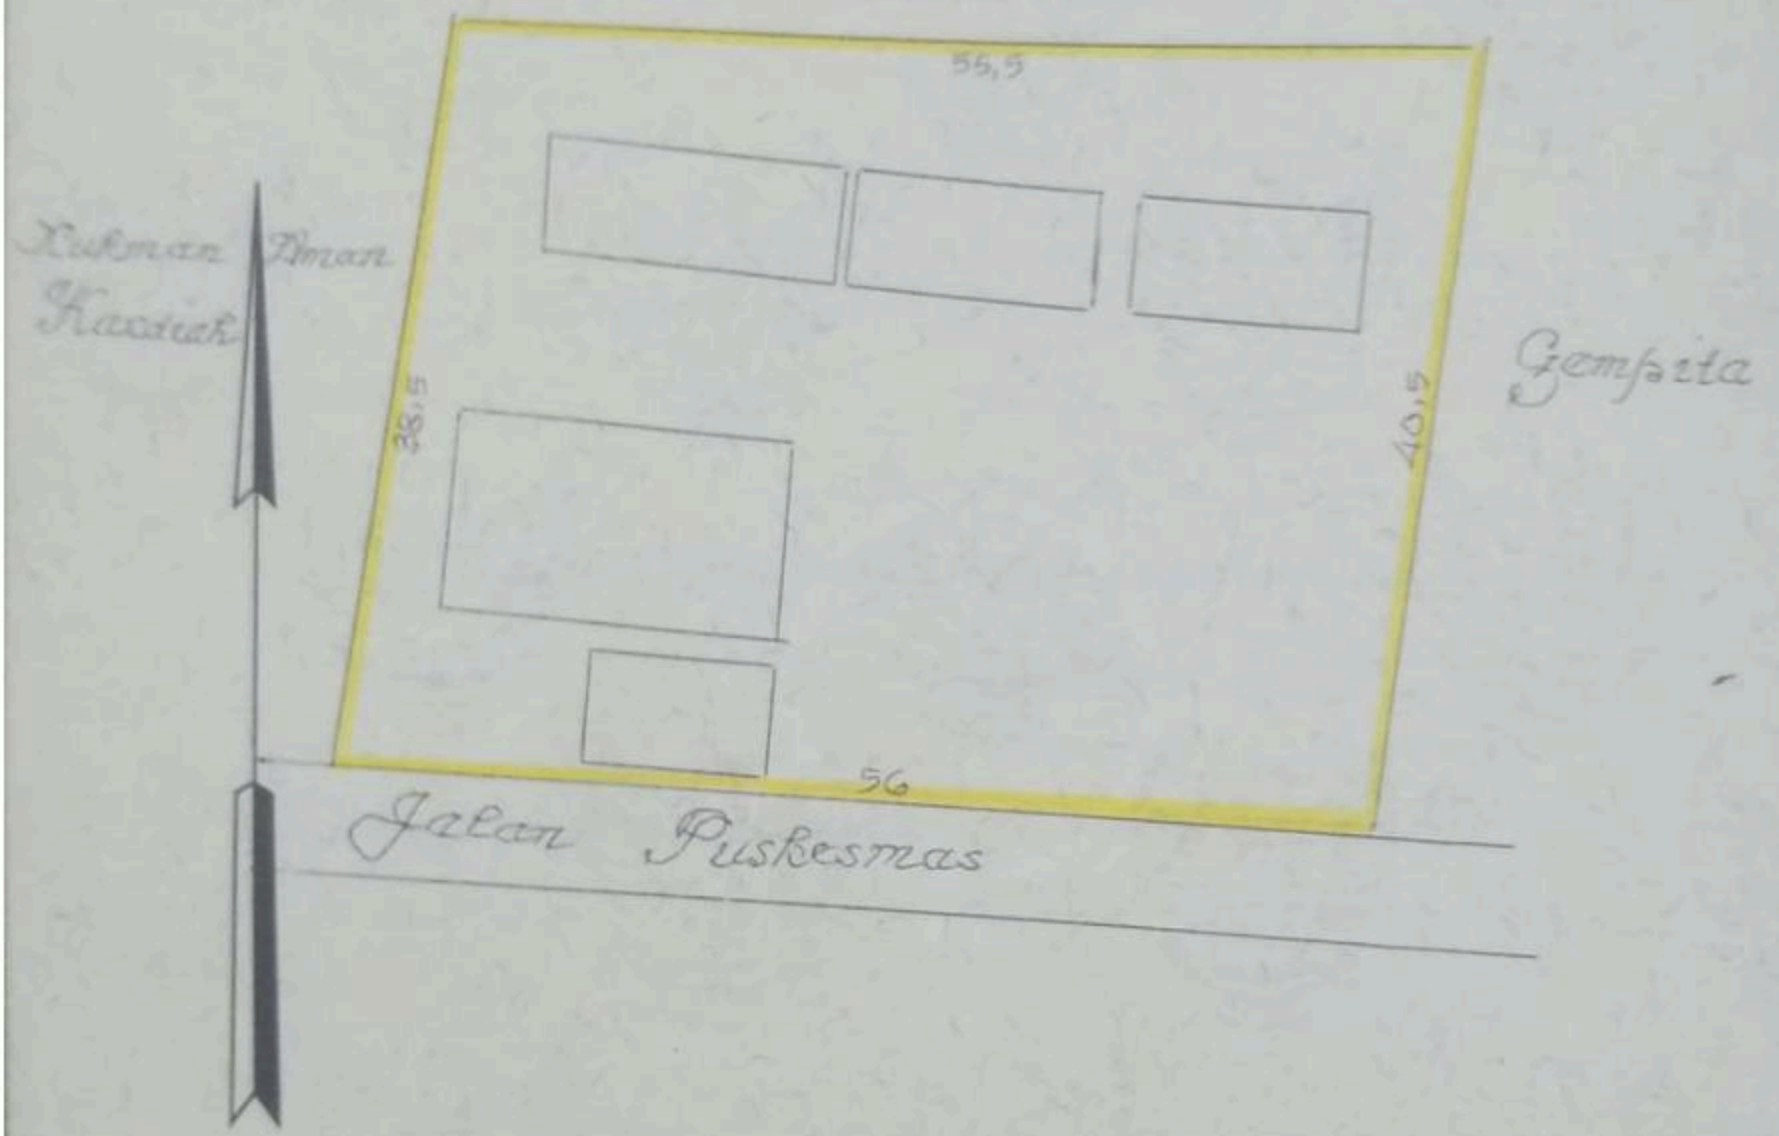

PENJELASAN : _____ batas tanah ini

Scanned with CamScanner

Hal lain - lain :

Daftar Isian 302 tgl. 8 Januari 2003 No. 8

Daftar Isian 307 tgl. ..... No. .....

UNTUK SERTIPIKAT

Takengon Tgl. *11 Januari* 200*2*

Takengon Tgl. *27 Pebruari* 200*3*

Kepala Seksi Pengukuran dan Pendaftaran Tanah

Kepala Kantor Pertanahan
Kabupaten / Kotamadya
Aceh Tengah

Kantor Pertanahan
Kabupaten / Kotamadya
Aceh Tengah

ttd.

DRS. HUDI YAZIR

NIP 010 172 837

= ZAHARI, SH =

NIP 010 104 801

Lihat surat ukur Pemisahan / Penggabungan / Penggantii Nomor ..... / 200.. Nomor hak : .....

Dikeluarkan surat ukur		Luas	Nomor hak	Sisa luas
Tanggal	Nomor			

Sisanya diuraikan dalam surat ukur Nomor : ..... / 200..... Nomor hak .....

Scanned with CamScanner