PUSKESMAS
RUSIP

BH 606214

DAFTAR ISIAN 206

BADAN PERTANAHAN NASIONAL
REPUBLIK INDONESIA

DINKES

8



SERTIPIKAT

(TANDA BUKTI HAK)

KANTOR PERTANAHAN
KABUPATEN / KOTA

.....

Kec.	**: Kec. Rusip Antara**
No. Urut	**: 8**
Alamat	: Rusip
No. Sertifikat	: 01.09.21.01.1.00005
Tahun	: 31 Desember 2009
Peruntukan	: Puskesmas Rusip
SKPK	**: Dinas Kesehatan**

0	1	•	0	9	•	2	1	•	0	1	•	1	•	0	0	0	0	5		

BH 606214

DAFTAR ISIAN 206

BADAN PERTANAHAN NASIONAL REPUBLIK INDONESIA



SERTIPIKAT

HAK : PAKAI No. 05

PROVINSI : ACEH

KABUPATEN / KOTA : ACEH TENGAH

KECAMATAN : RUSIP ANTARA

DESA/ KELURAHAN : RUSIP

DAFTAR ISIAN 307
No. .....

DAFTAR ISIAN 208
No. 7704 /2009

KANTOR PERTANAHAN
KABUPATEN / KOTA

ACEH TENGAH

0	1	•	0	9	•	2	1	•	0	1	•	1	•	0	0	0	0	5		

PENDAFTARAN - PERTAMA

Halaman :

a) HAK : PAKAI
No. : 05
Desa / Kel. : Rusip
Tgl. berakhirnya hak :

b) NIB 01.09.21.01.00007
Letak Tanah

f) NAMA PEMEGANG HAK

PEMERINTAH KABUPATEN ACEH TENGAH

Tanggal lahir / akta pendirian

c) ASAL HAK

1. Konversi

2. Pemberian hak Pakai

3. Pemecahan / Pemisahan / Penggabungan bidang

g) PEMBUKUAN

Takengon Tgl. 31 Desember 2009
Kepala Kantor Pertanahan
Kabupaten / Kota
Aceh Tengah

ttd.

DRS. HAMDAN

NIP 195411071978031002

d) DASAR PENDAFTARAN

1. Daftar Isian 202
Tgl.
No.

2. Surat Keputusan
Tgl.
No. 15 Desember 2009
45 / HP/ BPN/2008

3. Permohonan Pemecahan / Pemisahan / Penggabungan bidang
Tgl.
No.

h) PENERBITAN SERTIPIKAT

Takengon Tgl. 31 Desember 2009

Kepala Kantor Pertanahan
Kabupaten / Kota
Aceh Tengah

DRS. HAMDAN

NIP 195411071978031002

e) SURAT UKUR

Tgl. 09 Desember 2008
No. 02 /2008
Luas. 3.674 M2

i) PENUNJUK

BH 606214

DAFTAR ISIAN 207

0	1	•	0	9	•	8	1	•	0	1	•	1	•	0	0	0	0	5

NIB : 01.09.21.01.00007

SURAT UKUR

Nomor : 02 /2008

SEBIDANG TANAH TERLETAK DALAM

Provinsi : Aceh

Kabupaten / Kota : Aceh Tengah

Kecamatan : Rusip Antara

Desa /Kelurahan : Rusip

Peta : Nomor Peta Pendaftaran :

Lembar : Kotak :


Keadaan Tanah : Sebidang tanah digunakan Untuk Pembangunan Puskesmas Rusip

Tanda-tanda batas :

Luas : 3.674 M2 (Tiga ribu enam ratus tujuh puluh empat meter persegi)

Penunjukan dan penetapan batas : Ir. H. Nasaruddin, MM

SKALA 1 : 1000

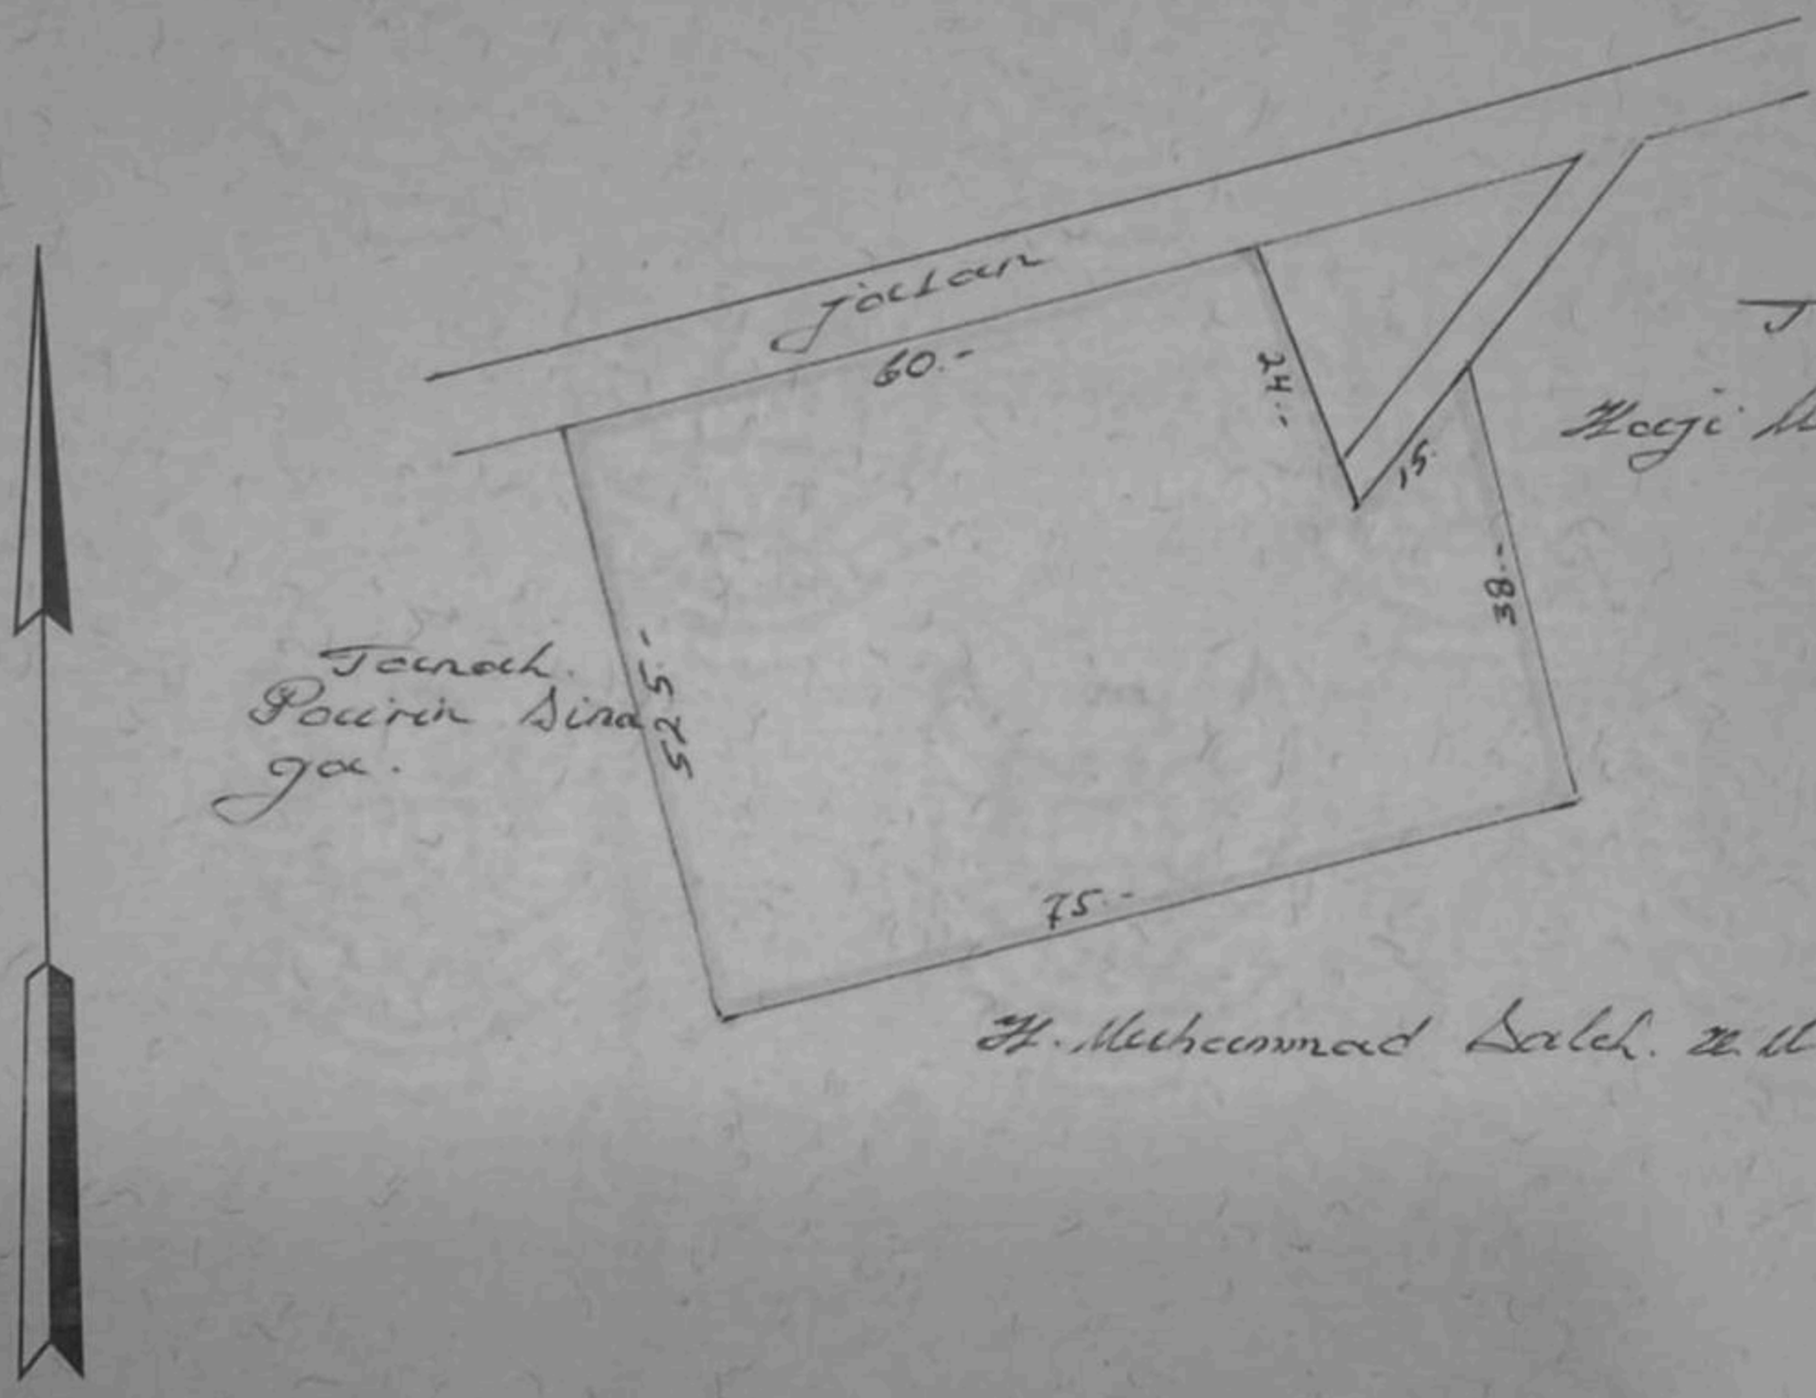

PENJELASAN : ..... batas tanah ini

Hal lain - lain :

Daftar Isian 302 tgl. No.

Daftar Isian 307 tgl. No.

Tanggal Penomoran Surat Ukur

UNTUK SERTIPIKAT

Takengon Tgl. 31 Desember 2009

Kepala Kantor Pertanahan
Kabupaten / Kota
Aceh Tengah

DRS. HAMDAN

NIP *19541107 1978031002*

Takengon Tgl. 09 Desember 2008

Kepala Seksi Survei, Pengukuran dan Pemetaan

Kantor Pertanahan
Kabupaten / Kota
Aceh Tengah

ttd

ERWIS, APtnh

NIP *19650607 198603 1 003*

Lihat surat ukur Pemisahan / Penggabungan / Pengganti

Nomor : Nomor hak :

Dikeluarkan surat ukur		Luas	Nomor hak	Sisa luas
Tanggal	Nomor			

Sisanya diuraikan dalam surat ukur Nomor : Nomor hak :